

## Rénovation d'une habitation

MAITRES D'OUVRAGE :

Céline et Amir ROCHE-SHAHAM  
5 rue Beausoleil  
CESSON-SEVIGNÉ

# APPEL D'OFFRES AUX ENTREPRISES


Le 06.05.2026

## DOSSIER DE PLANS



Charlie FRALEUX - 06.68.07.63.68  
charlie@atelierfralex.fr




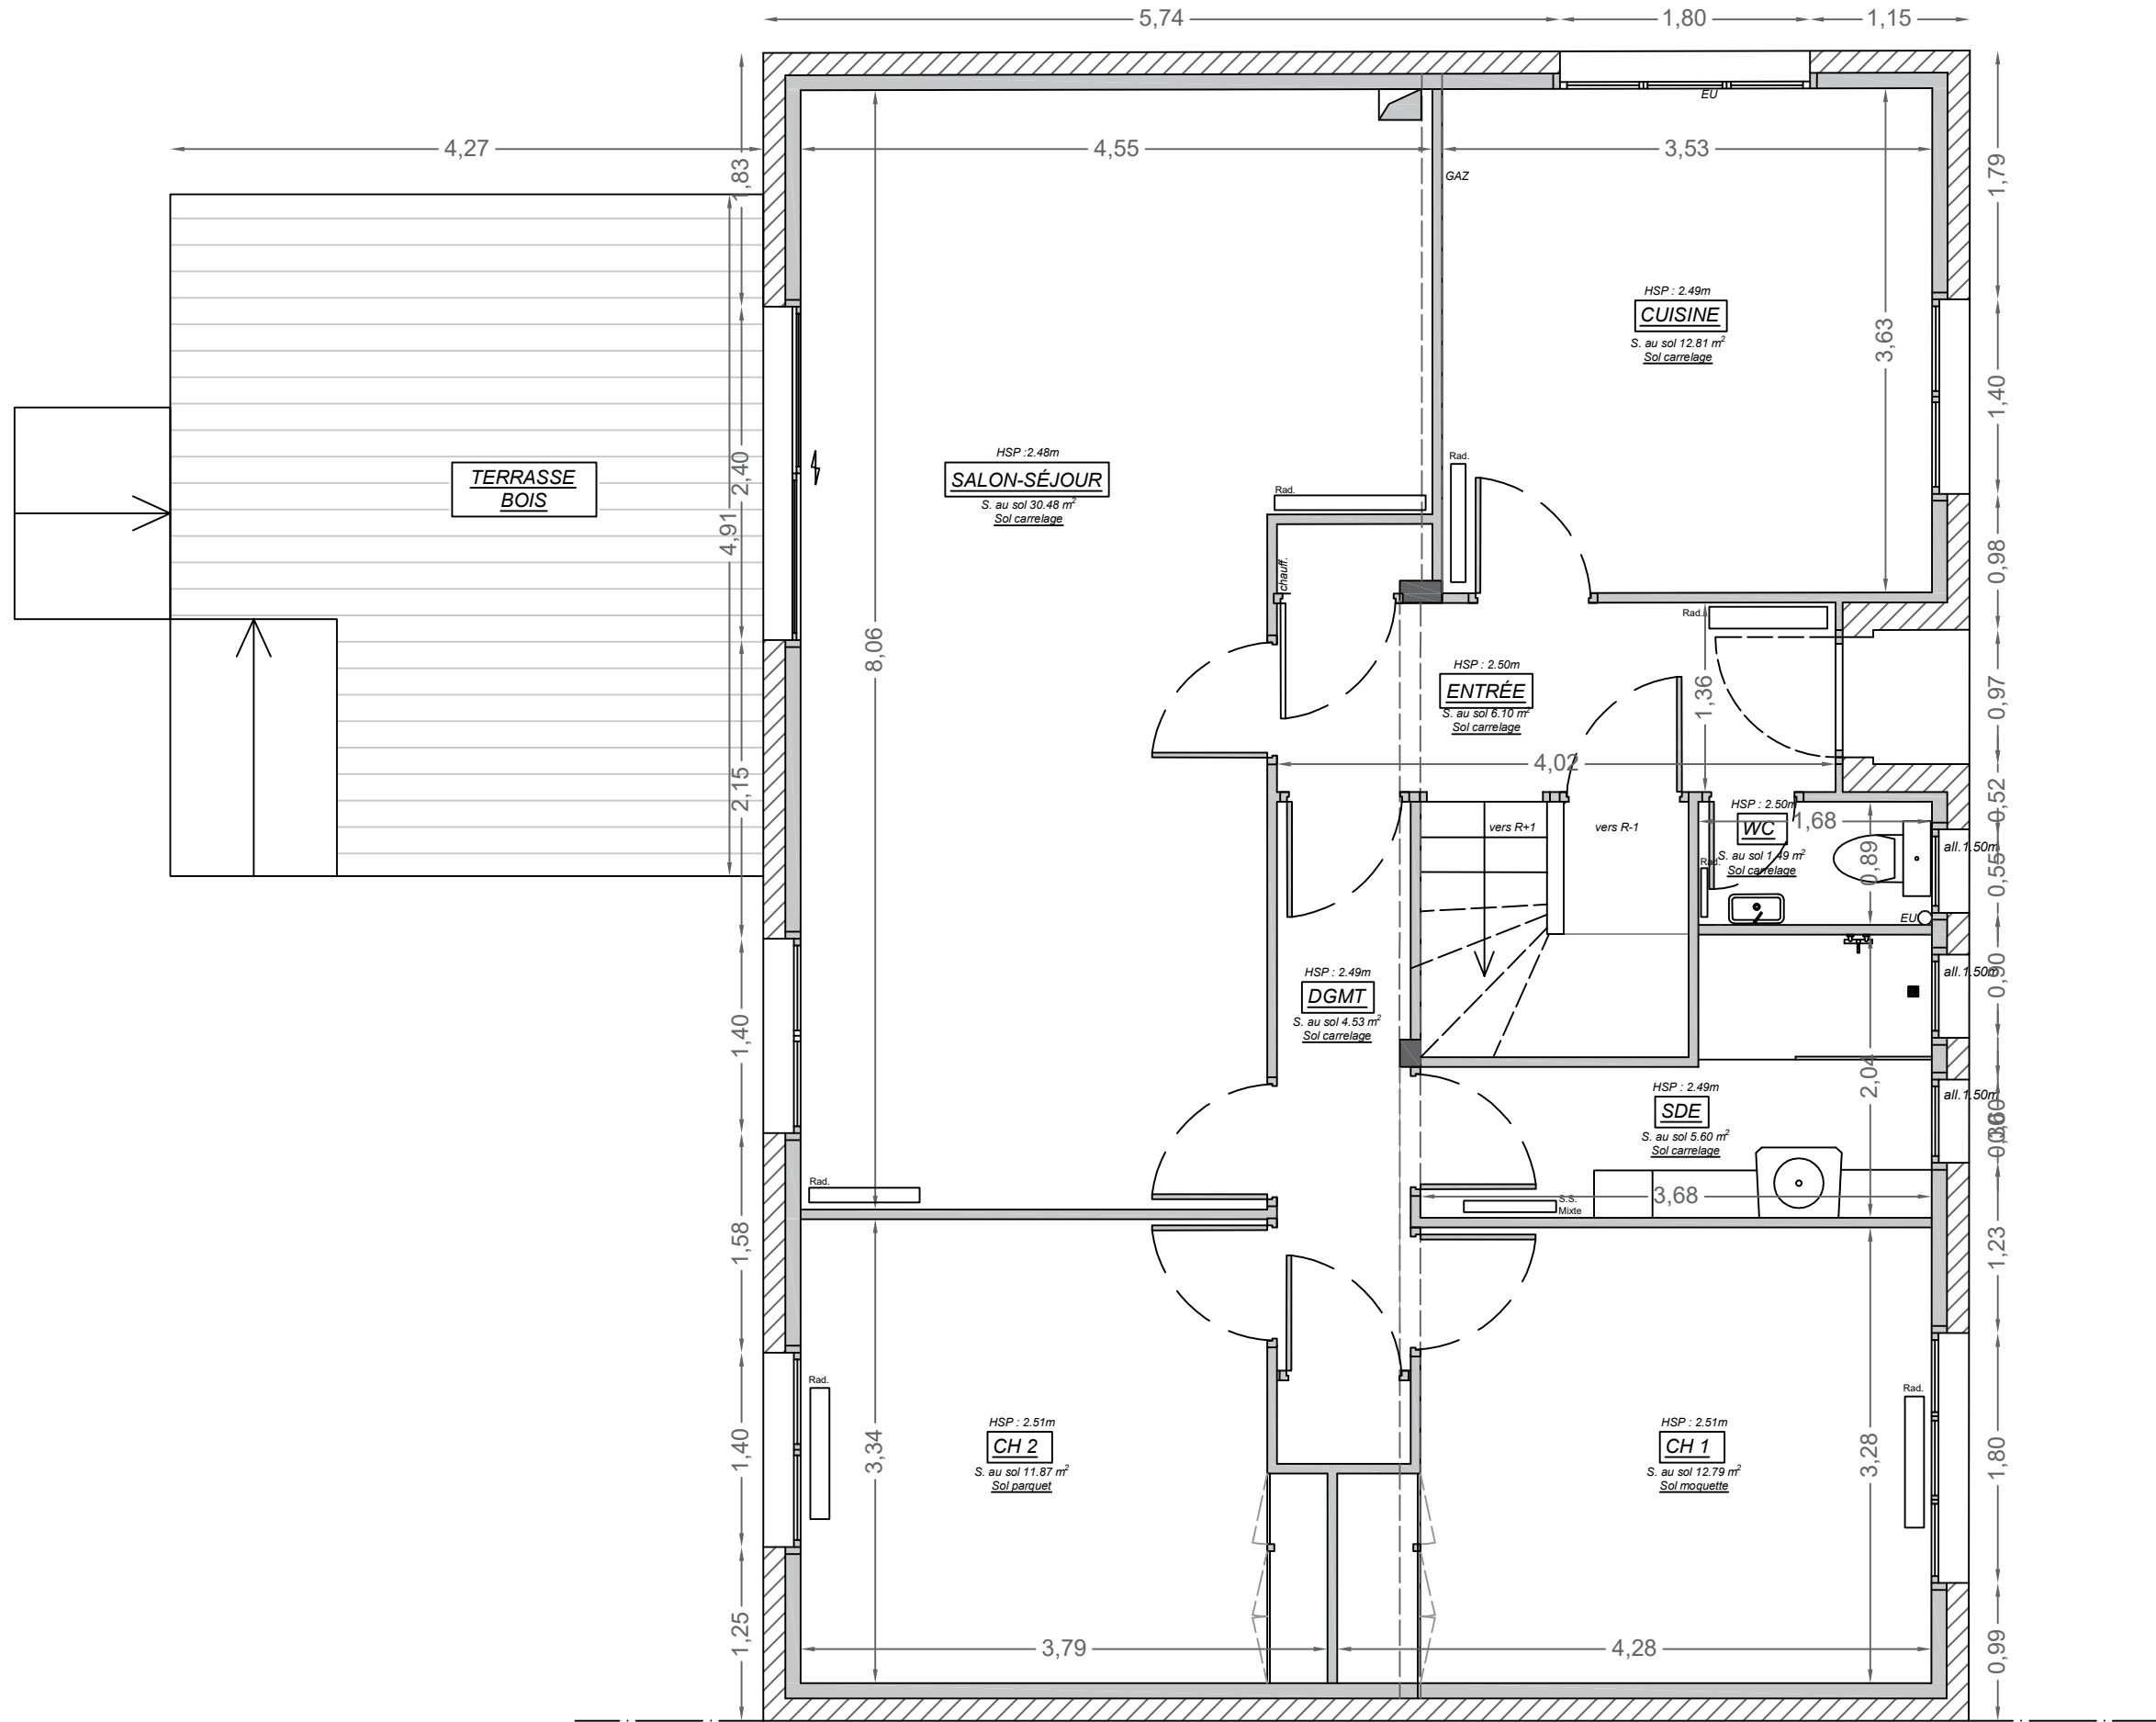




|                                                                                                   |  |                                                                                                |                         |                |   |
|---------------------------------------------------------------------------------------------------|--|------------------------------------------------------------------------------------------------|-------------------------|----------------|---|
| PROJET : Rénovation d'une habitation                                                              |  |                                                                                                |                         | PHASE :<br>APO | N°page:<br>2   |
| PLAN RDC - EXISTANT                                                                               |  | Date :<br>05/05/2026                                                                           | Echelle :<br>1/50e - A3 | Indice : 1     | Charlie FRALEUX<br>06.68.07.63.68<br><br><small>Ces plans ne sont pas des plans techniques de chantier et ne peuvent être utilisés en phase EXE.<br/>Les cotes doivent être reprises par les lots concernés avant l'exécution de leurs ouvrages.</small> |
| MAITRE D'OUVRAGE :<br><br>Céline et Amir ROCHE-SHAHAM<br>5 rue Beausoleil<br>35510 CESSON-SEVIGNÉ |  | MAITRE D'OEUVRE :<br><br>ATELIER FRALEUX<br>19 rue de la Croix Verte<br>ST JACQUES DE LA LANDE |                         |                |   |
|                                                                                                   |  |                                                                                                |                         |                |   |

Atelier  
Fraleux

- ARCHITECTURE INTÉRIEURE -  
- MAÎTRISE D'OEUVRE -

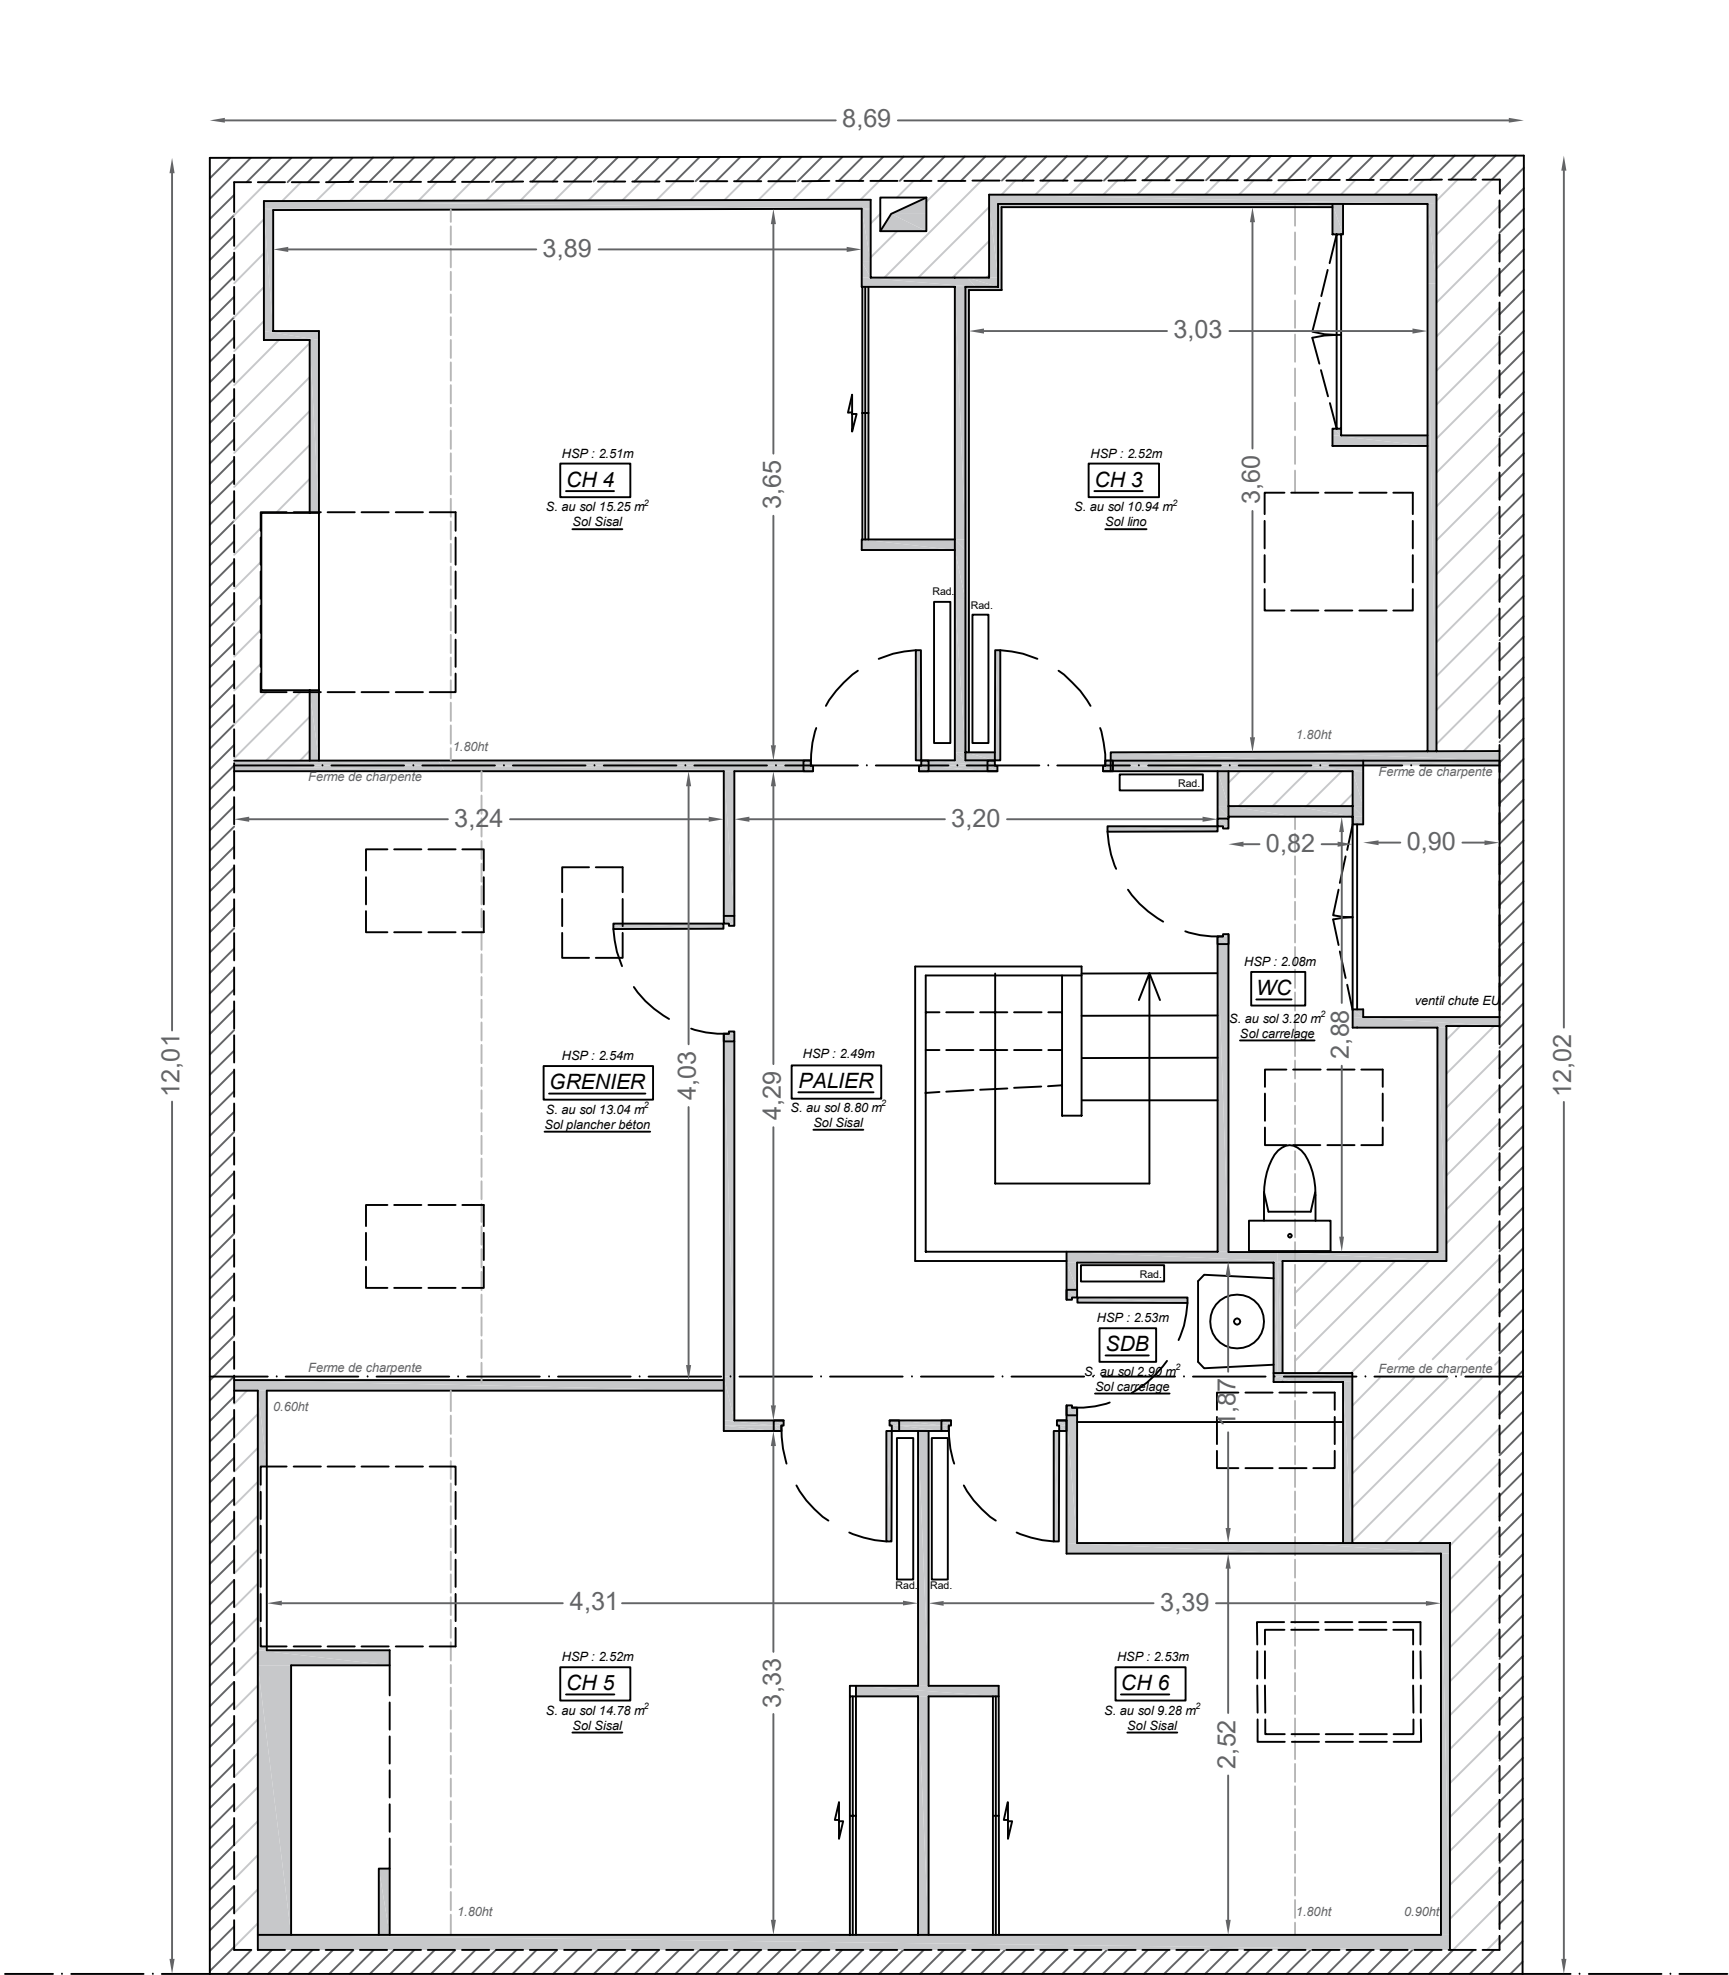

|                                                                                                   |                     |                                                                                                |   |  |
|---------------------------------------------------------------------------------------------------|---------------------|------------------------------------------------------------------------------------------------|---|--|
| PHASE :<br>APO                                                                                    |                     |                                                                                                | N°page:<br>3   |  |
| PROJET : Rénovation d'une habitation                                                              |                     | Indice : 1                                                                                     | Charlie FRALEUX<br>06.68.07.63.68   |  |
|                                                                                                   |                     | Echelle :<br>1/50e - A3                                                                        |   |  |
|                                                                                                   | PLAN R+1 - EXISTANT | Date :<br>05/05/2026                                                                           | Ces plans ne sont pas des plans techniques de chantier et ne peuvent être utilisés en phase EXE.<br>Les cotes doivent être reprises par les lots concernés avant l'exécution de leurs ouvrages. |  |
| MAITRE D'OUVRAGE :<br><br>Céline et Amir ROCHE-SHAMAM<br>5 rue Beausoleil<br>35510 CESSON-SEVIGNÉ |                     | MAITRE D'OEUVRE :<br><br>ATELIER FRALEUX<br>19 rue de la Croix Verte<br>ST JACQUES DE LA LANDE |   |  |
| <div>Atelier<br/>Fraleux</div> <div>- ARCHITECTURE INTÉRIEURE -<br/>- MAÎTRISE D'OEUVRE -</div>   |                     |                                                                                                |   |  |

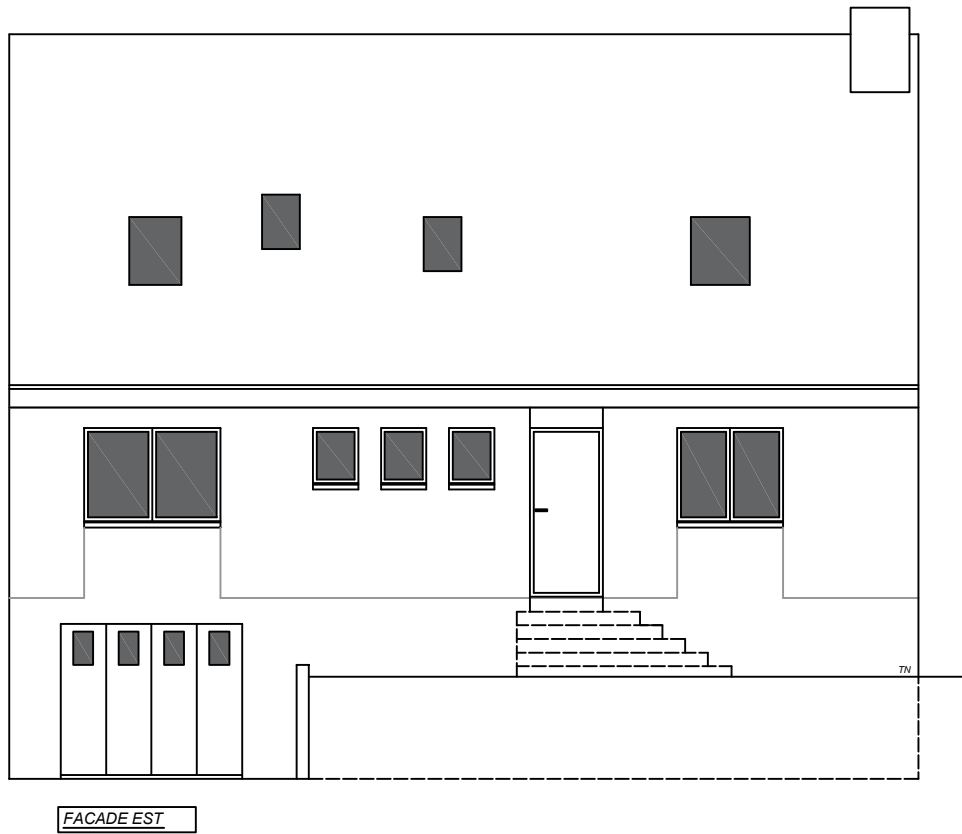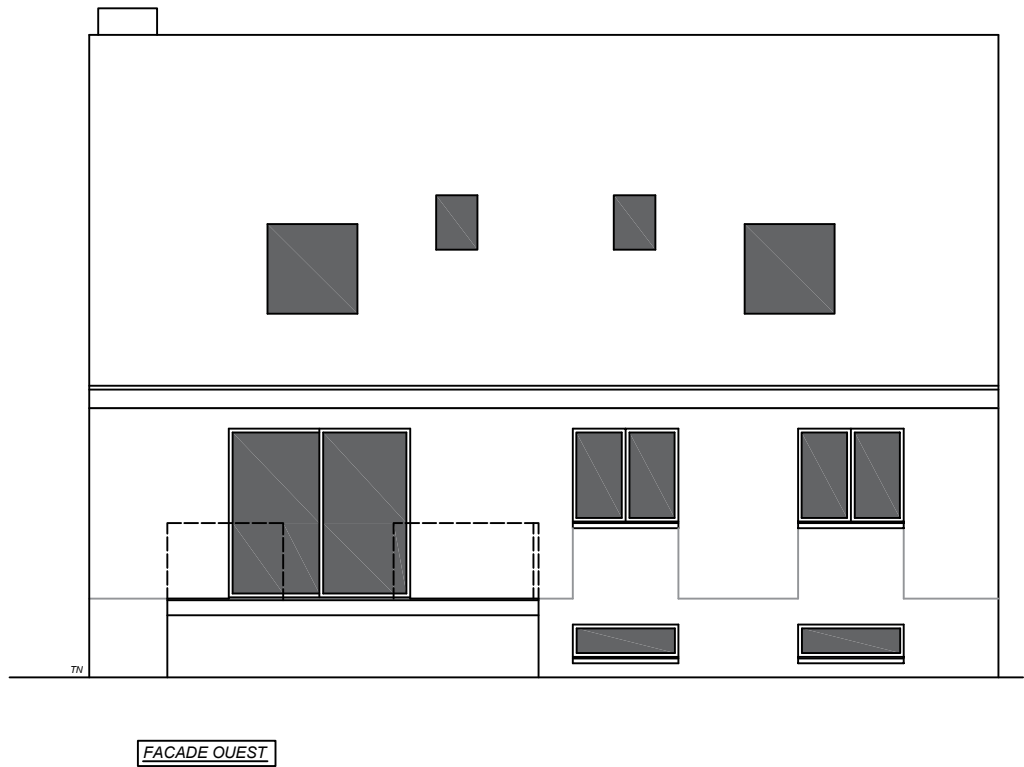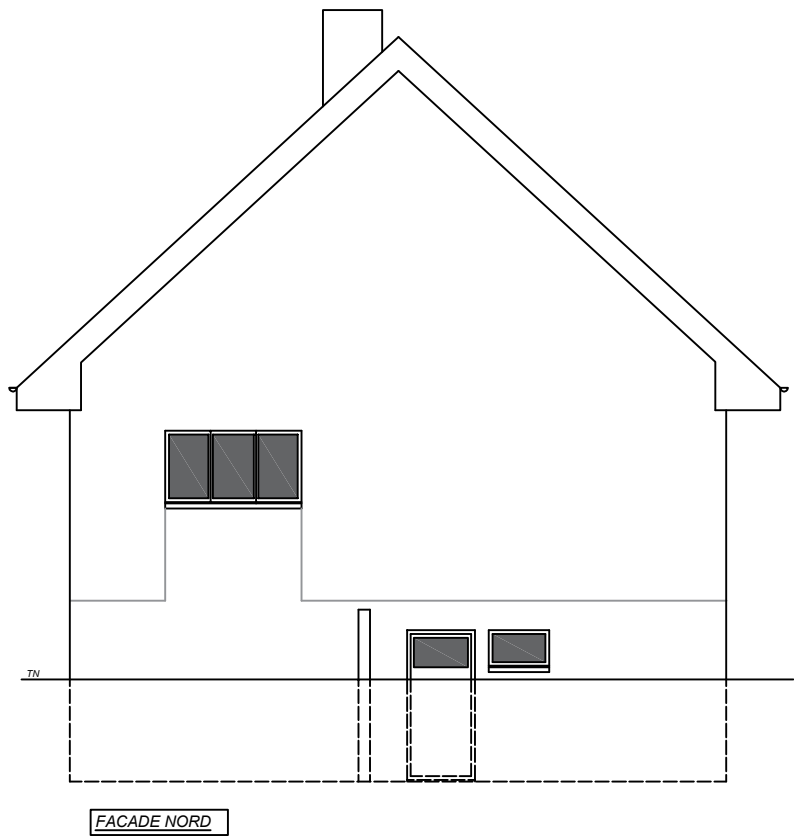

|                                                                                                   |  |   |                          |                |   |
|---------------------------------------------------------------------------------------------------|--|---|--------------------------|----------------|---|
| PROJET : Rénovation d'une habitation                                                              |  |   |                          | PHASE :<br>APO | N°page:<br>4   |
| FACADES - EXISTANT                                                                                |  | Date :<br>05/05/2026                                                                                  | Echelle :<br>1/100e - A3 | Indice : 1     | Charlie FRALEUX<br>06.68.07.63.68<br><br><small>Ces plans ne sont pas des plans techniques de chantier et ne peuvent être utilisés en phase EXE.<br/>Les cotes doivent être reprises par les lots concernés avant l'exécution de leurs ouvrages.</small> |
| MAITRE D'OUVRAGE :<br><br>Céline et Amir ROCHE-SHAMAM<br>5 rue Beausoleil<br>35510 CESSON-SEVIGNÉ |  | MAITRE D'OEUVRE :<br><br><u>ATELIER FRALEUX</u><br>19 rue de la Croix Verte<br>ST JACQUES DE LA LANDE |                          |                |   |
|                                                                                                   |  |   |                          |                |   |

Atelier  
Fraleux

- ARCHITECTURE INTÉRIEURE -  
- MAÎTRISE D'OEUVRE -



Vue de la rue Beausoleil




Vue depuis le jardin

|   |  |  |                                                                                                |              |  |
|---|--|--|------------------------------------------------------------------------------------------------|--------------|--|
| PHASE :<br>APO   |  |  |                                                                                                | N°page:<br>5 |  |
| PROJET : Rénovation d'une habitation   |  |  |                                                                                                |              |  |
|   |  |  |                                                                                                |              |  |
| PHOTOGRAPHIES - EXISTANT   |  |  | Date :<br>05/05/2026                                                                           |              |  |
| MAITRE D'OUVRAGE :<br><br>Céline et Amir ROCHE-SHAMAM<br>5 rue Beausoleil<br>35510 CESSON-SEVIGNÉ                                                                                            |  |  | MAITRE D'OEUVRE :<br><br>ATELIER FRALEUX<br>19 rue de la Croix Verte<br>ST JACQUES DE LA LANDE |              |  |
| Charlie FRALEUX<br>06.68.07.63.68   |  |  |                                                                                                |              |  |
| Ces plans ne sont pas des plans techniques de chantier et ne peuvent être utilisés en phase EXE. Les cotes doivent être reprises par les lots concernés avant l'exécution de leurs ouvrages. |  |  |                                                                                                |              |  |

Atelier  
Fraleux

- ARCHITECTURE INTÉRIEURE -  
- MAÎTRISE D'OEUVRE -

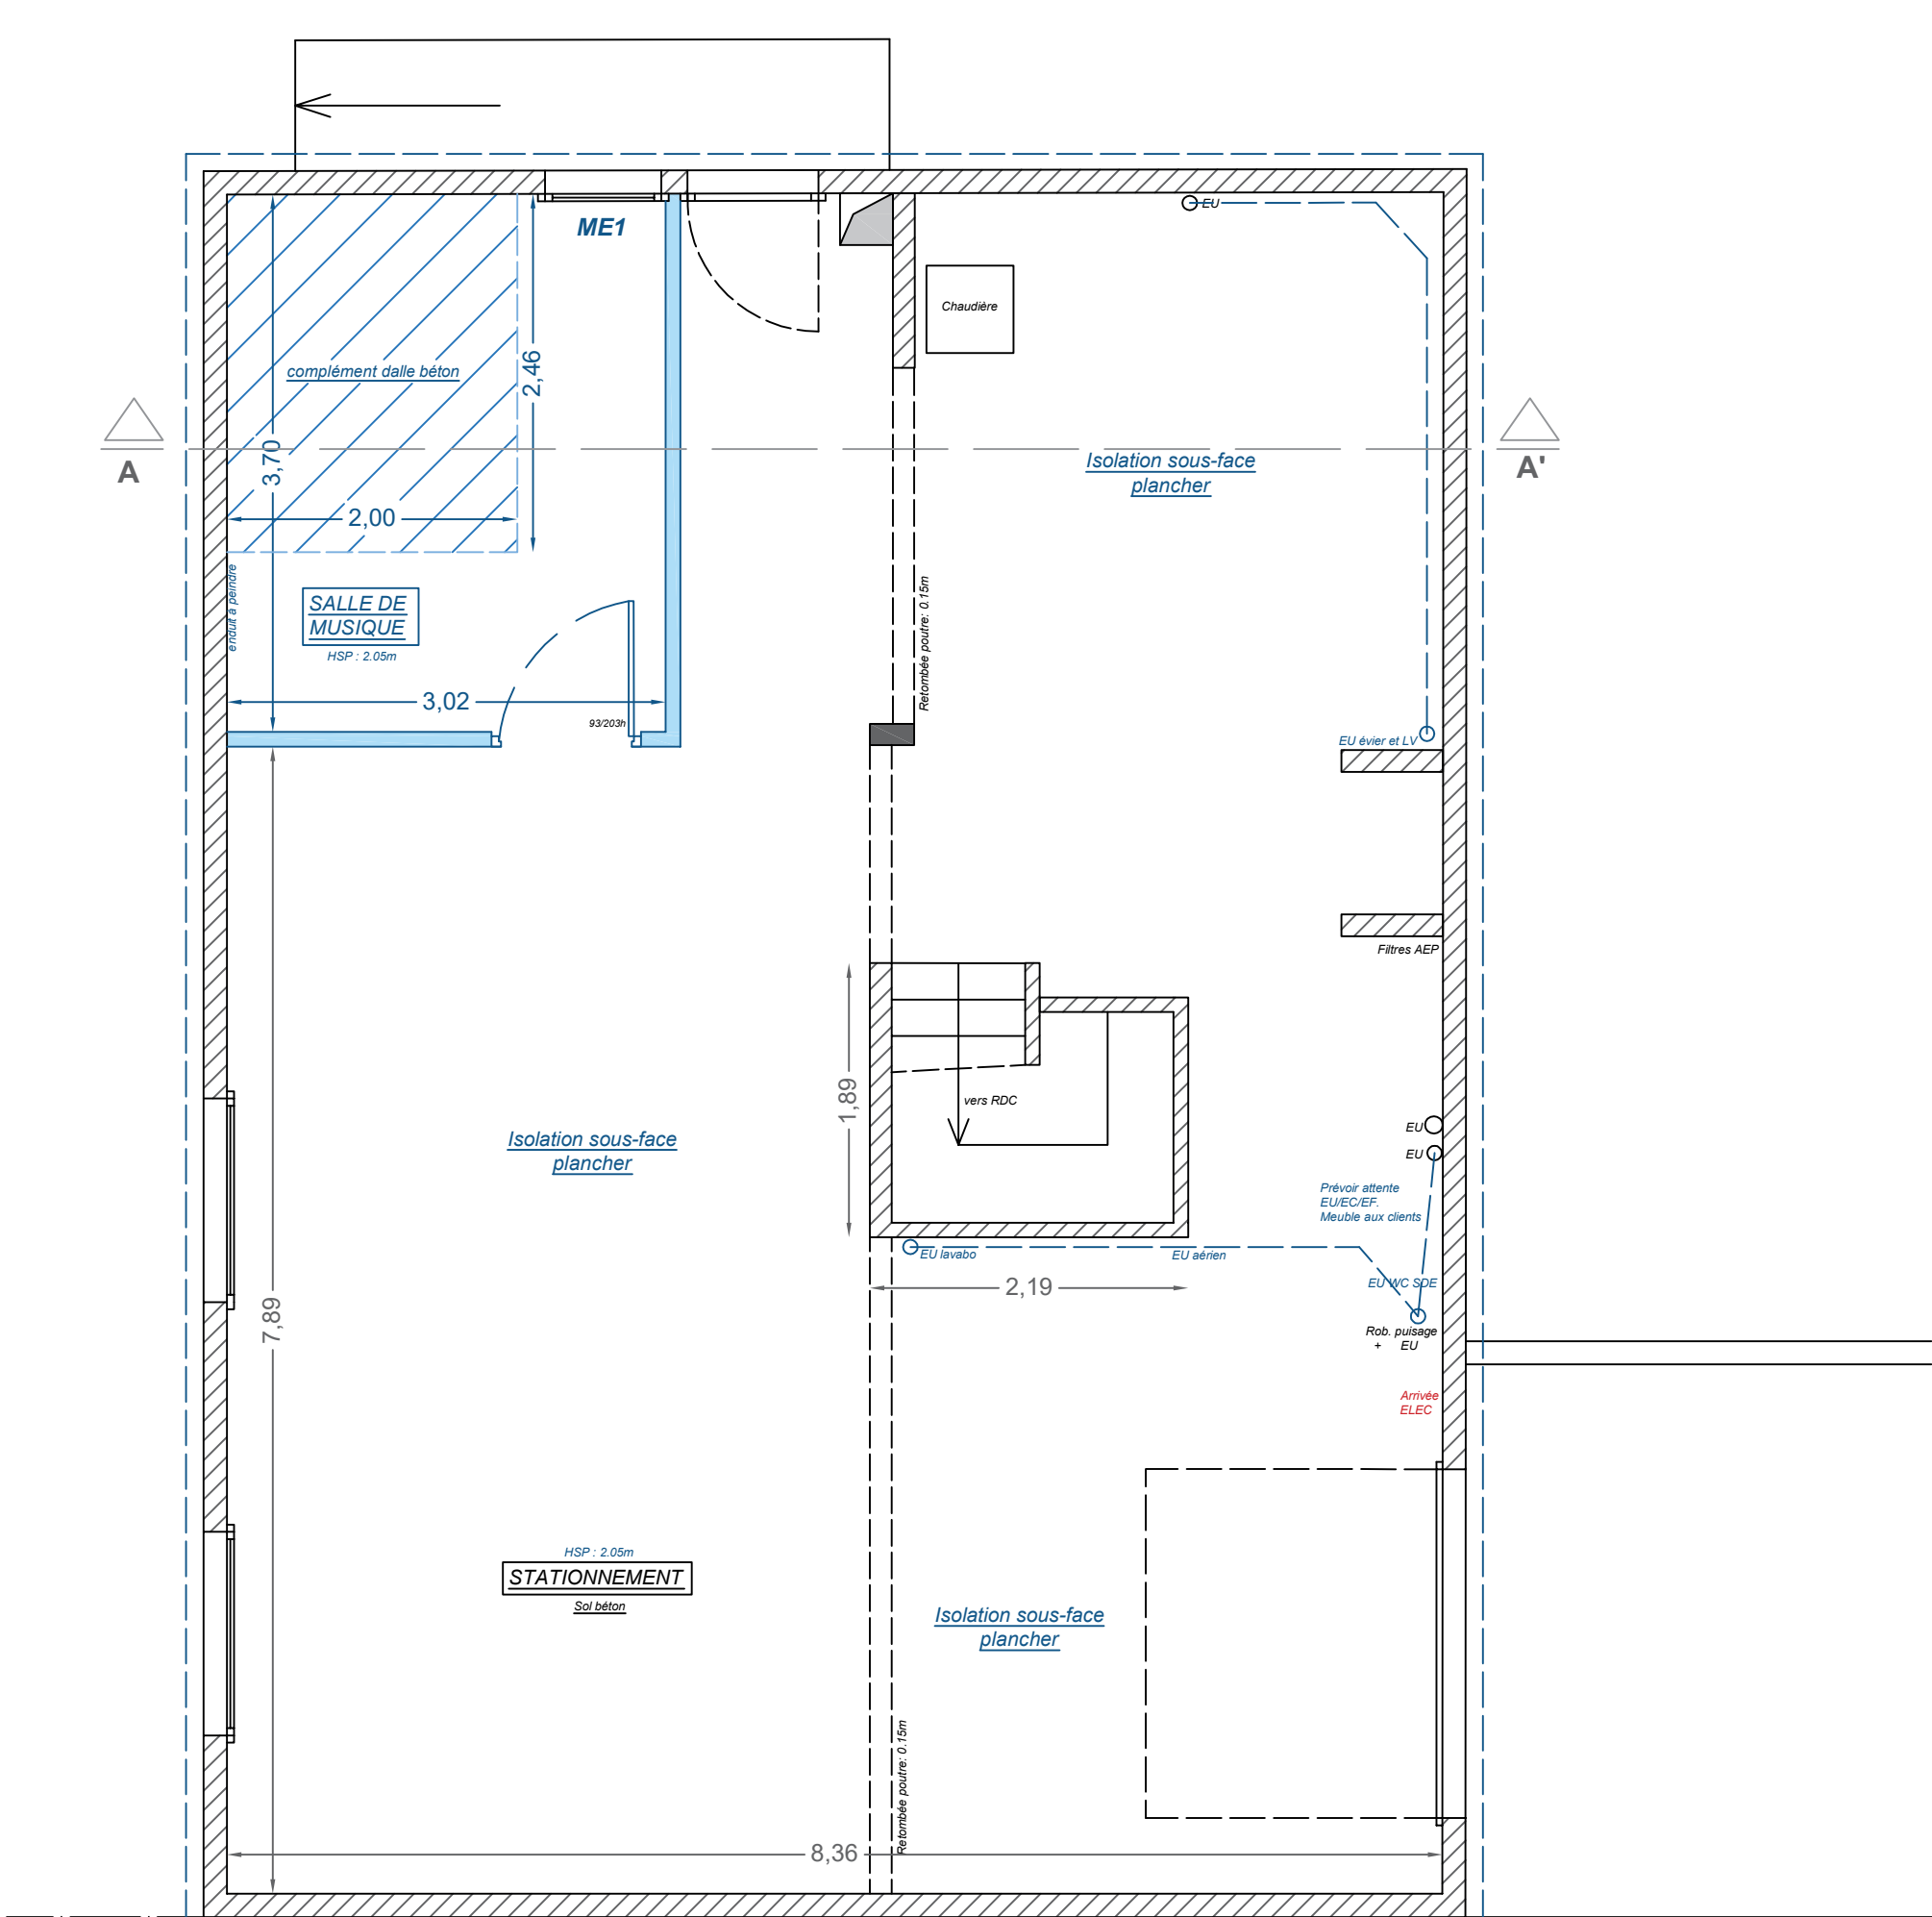

NORD




|                                                                                                   |                      |                                                                                                |                                   |   |
|---------------------------------------------------------------------------------------------------|----------------------|------------------------------------------------------------------------------------------------|-----------------------------------|---|
| PHASE :<br>APO                                                                                    |                      |                                                                                                | N°page:<br>6                      |   |
| PROJET : Rénovation d'une habitation                                                              | Indice : 1           | Echelle :<br>1/50e - A3                                                                        | Charlie FRALEUX<br>06.68.07.63.68 |   |
|                                                                                                   | Date :<br>05/05/2026 |                                                                                                |                                   |   |
|                                                                                                   | PLAN R-1 - PROJET    | MAITRE D'OEUVRE :<br><br>ATELIER FRALEUX<br>19 rue de la Croix Verte<br>ST JACQUES DE LA LANDE |                                   | Ces plans ne sont pas des plans techniques de chantier et ne peuvent être utilisés en phase EXE. Les cotes doivent être reprises par les lots concernés avant l'exécution de leurs ouvrages. |
| MAITRE D'OUVRAGE :<br><br>Céline et Amir ROCHE-SHAMAM<br>5 rue Beausoleil<br>35510 CESSON-SEVIGNÉ |                      |                                                                                                |                                   |   |

Atelier  
Fraleux

- ARCHITECTURE INTÉRIEURE -  
- MAÎTRISE D'OEUVRE -

bleu= projet

noir= existant

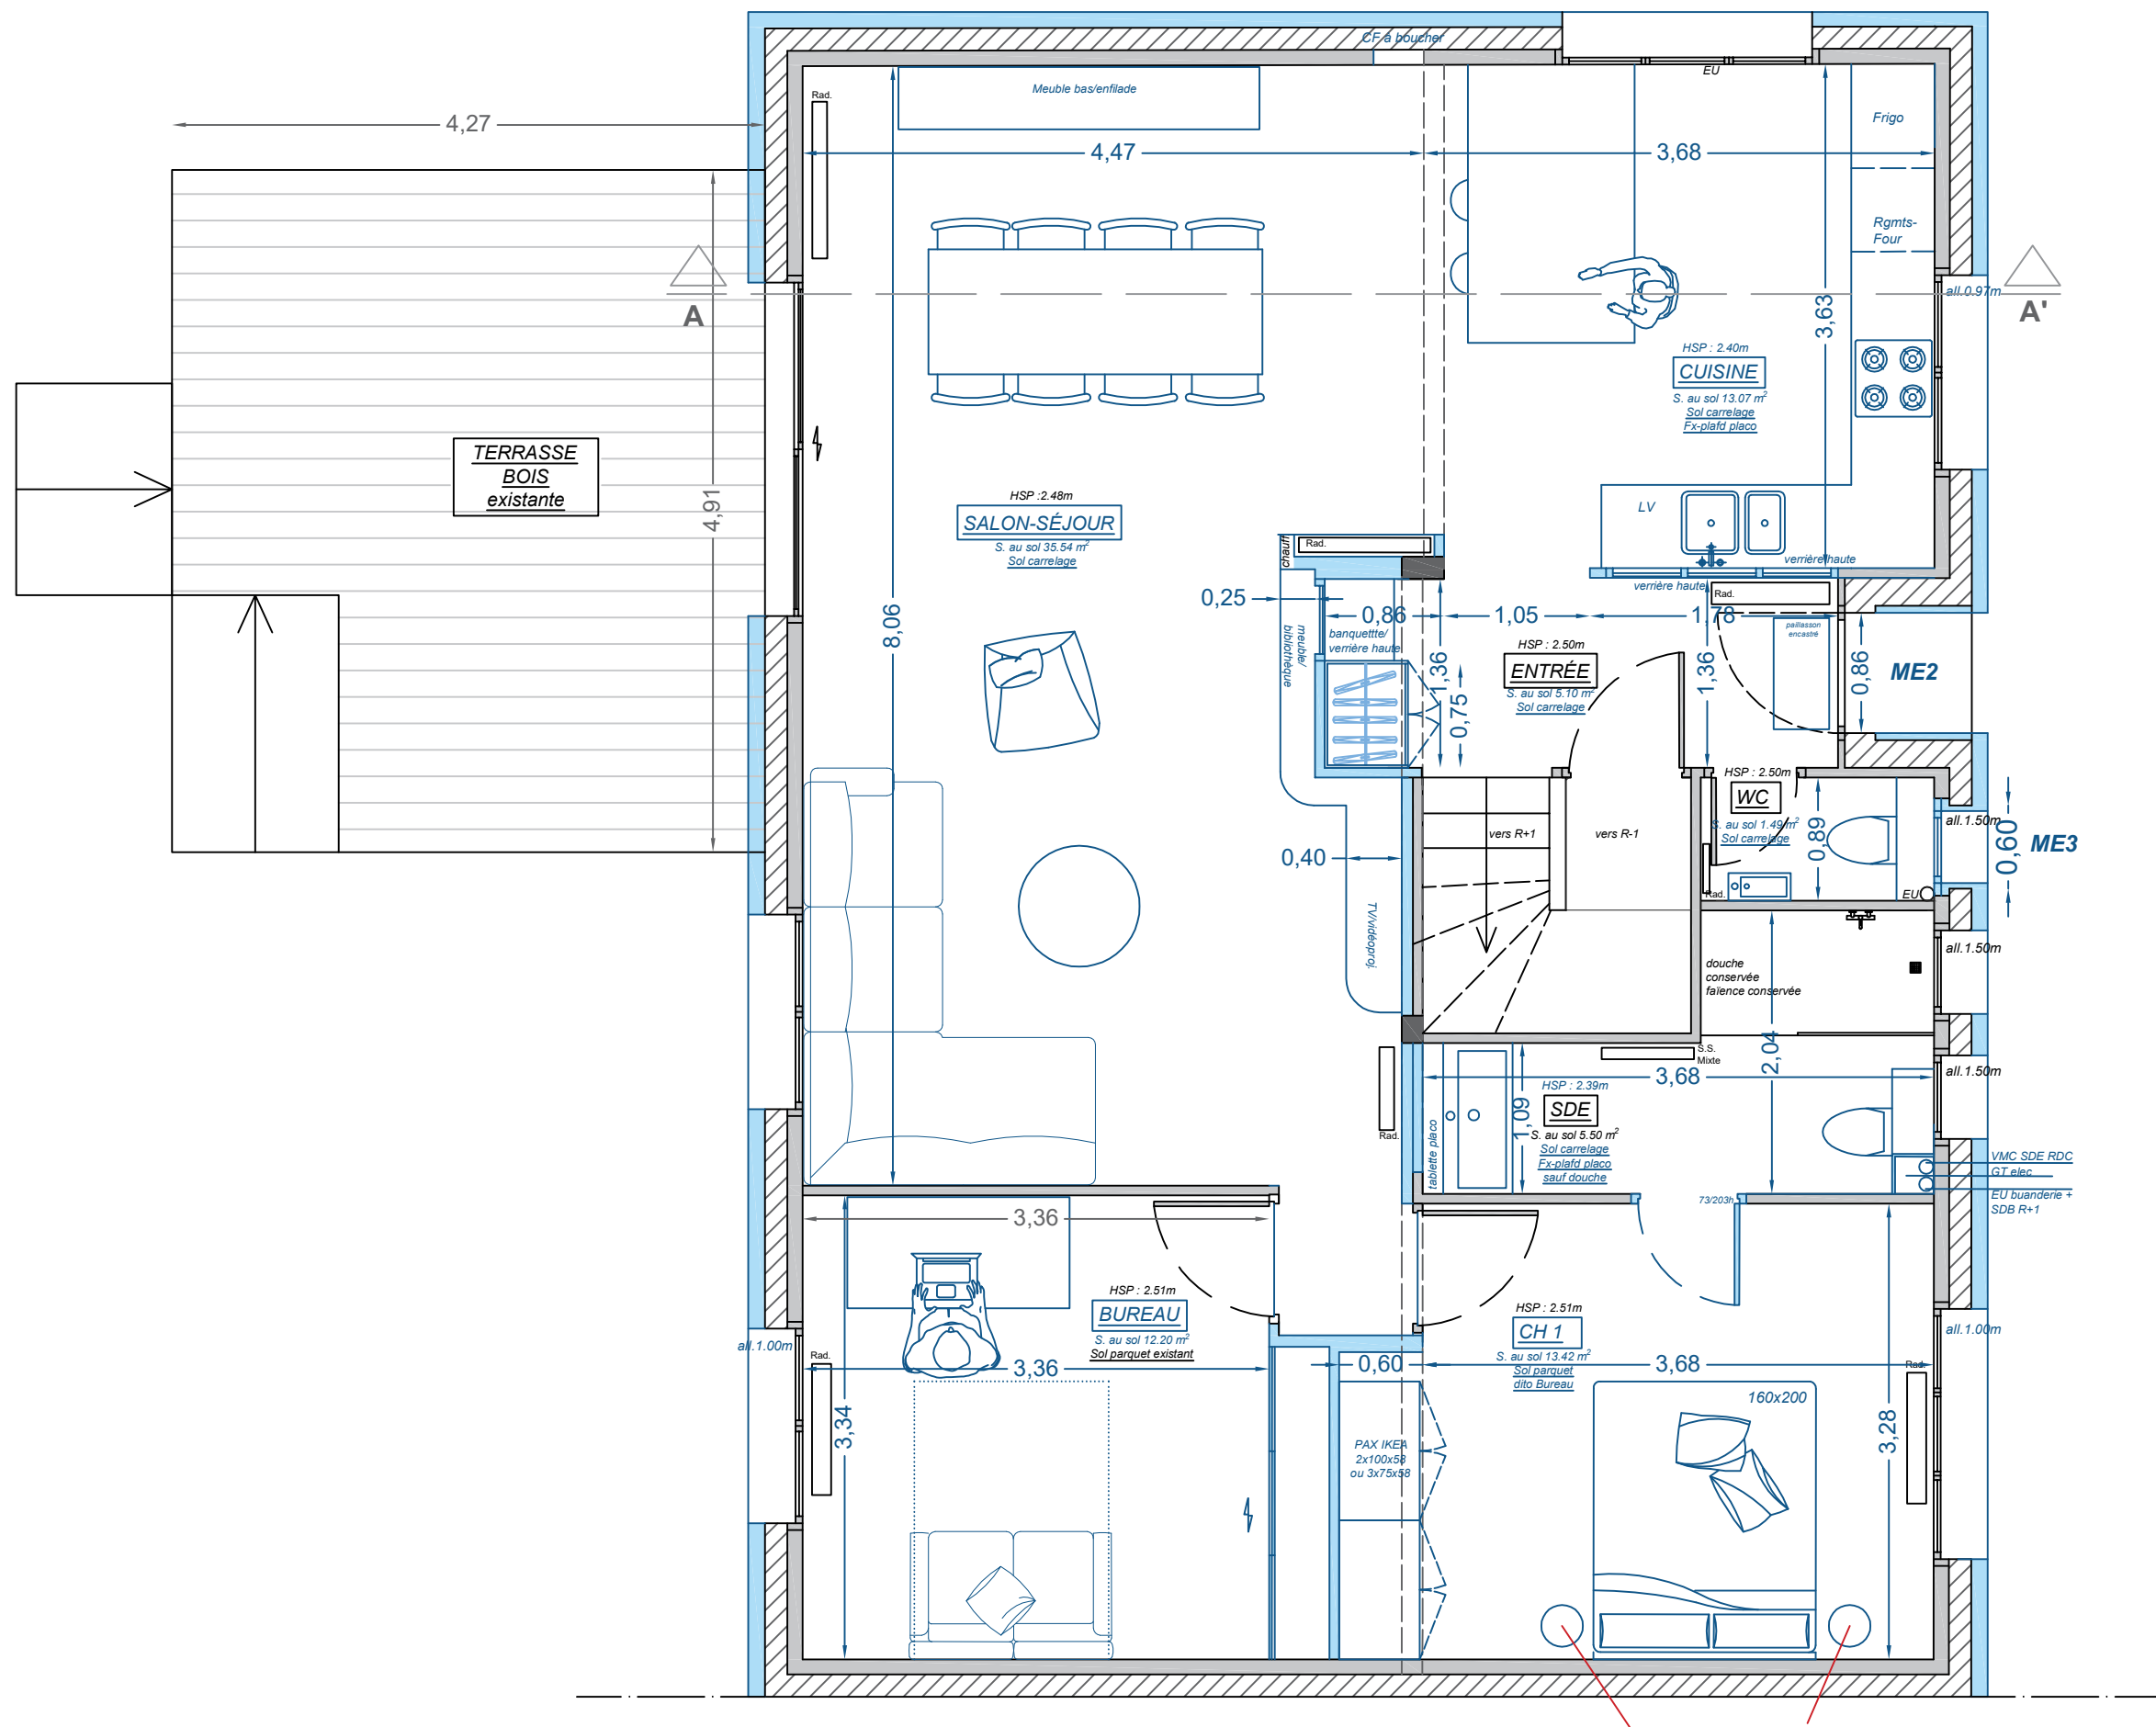


|                                      |                                                                                                   |                                                                                                |            |                                   |   |
|--------------------------------------|---------------------------------------------------------------------------------------------------|------------------------------------------------------------------------------------------------|------------|-----------------------------------|---|
| PROJET : Rénovation d'une habitation |                                                                                                   |                                                                                                |            | PHASE :<br>APO                    | N°page:<br>7   |
| PLAN RDC - PROJET                    | Date :<br>05/05/2026                                                                              | Echelle :<br>1/50e - A3                                                                        | Indice : 1 | Charlie FRALEUX<br>06.68.07.63.68 | Ces plans ne sont pas des plans techniques de chantier et ne peuvent être utilisés en phase EXE.<br>Les cotes doivent être reprises par les lots concernés avant l'exécution de leurs ouvrages. |
|                                      | MAITRE D'OUVRAGE :<br><br>Céline et Amir ROCHE-SHAHAM<br>5 rue Beausoleil<br>35510 CESSON-SEVIGNÉ | MAITRE D'OEUVRE :<br><br>ATELIER FRALEUX<br>19 rue de la Croix Verte<br>ST JACQUES DE LA LANDE |            |                                   |   |

Atelier  
Fraleux

- ARCHITECTURE INTÉRIEURE -  
- MAÎTRISE D'OEUVRE -

bleu= projet  
noir= existant

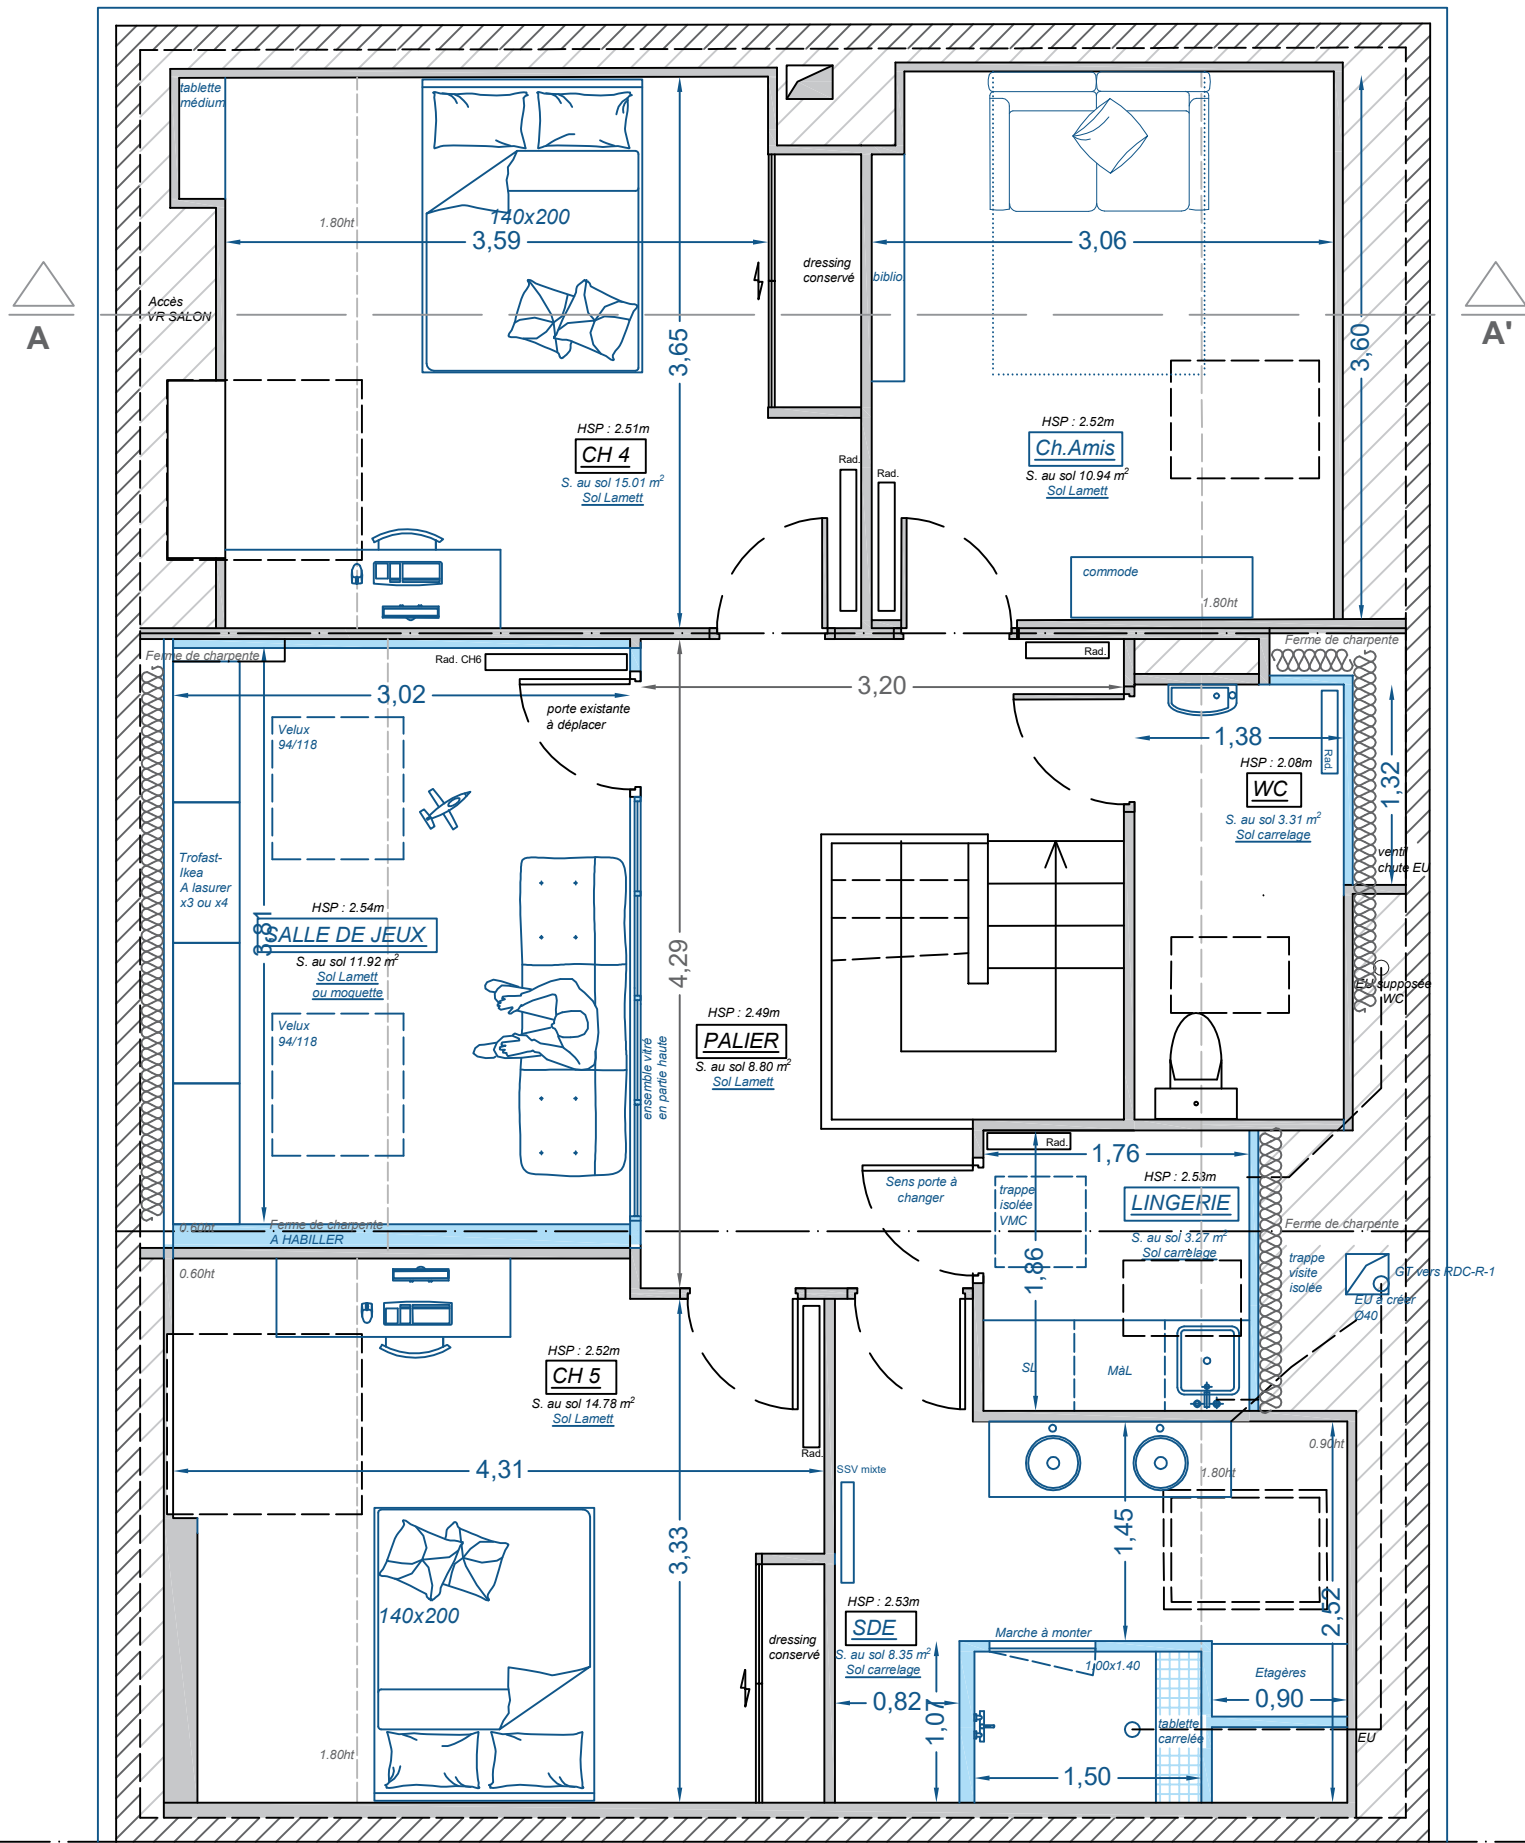


|                                                                                                   |  |                                                                                                |                         |                |   |
|---------------------------------------------------------------------------------------------------|--|------------------------------------------------------------------------------------------------|-------------------------|----------------|---|
| PROJET : Rénovation d'une habitation                                                              |  |                                                                                                |                         | PHASE :<br>APO | N°page:<br>8   |
| PLAN R+1 - PROJET                                                                                 |  | Date :<br>05/05/2026                                                                           | Echelle :<br>1/50e - A3 | Indice : 1     | Charlie FRALEUX<br>06.68.07.63.68<br><br><small>Ces plans ne sont pas des plans techniques de chantier et ne peuvent être utilisés en phase EXE.<br/>Les cotes doivent être reprises par les lots concernés avant l'exécution de leurs ouvrages.</small> |
| MAITRE D'OUVRAGE :<br><br>Céline et Amir ROCHE-SHAHAM<br>5 rue Beausoleil<br>35510 CESSON-SEVIGNÉ |  | MAITRE D'OEUVRE :<br><br>ATELIER FRALEUX<br>19 rue de la Croix Verte<br>ST JACQUES DE LA LANDE |                         |                |   |
|                                                                                                   |  |                                                                                                |                         |                |   |


Atelier  
Fraleux

- ARCHITECTURE INTÉRIEURE -  
- MAÎTRISE D'OEUVRE -

bleu= projet  
noir= existant

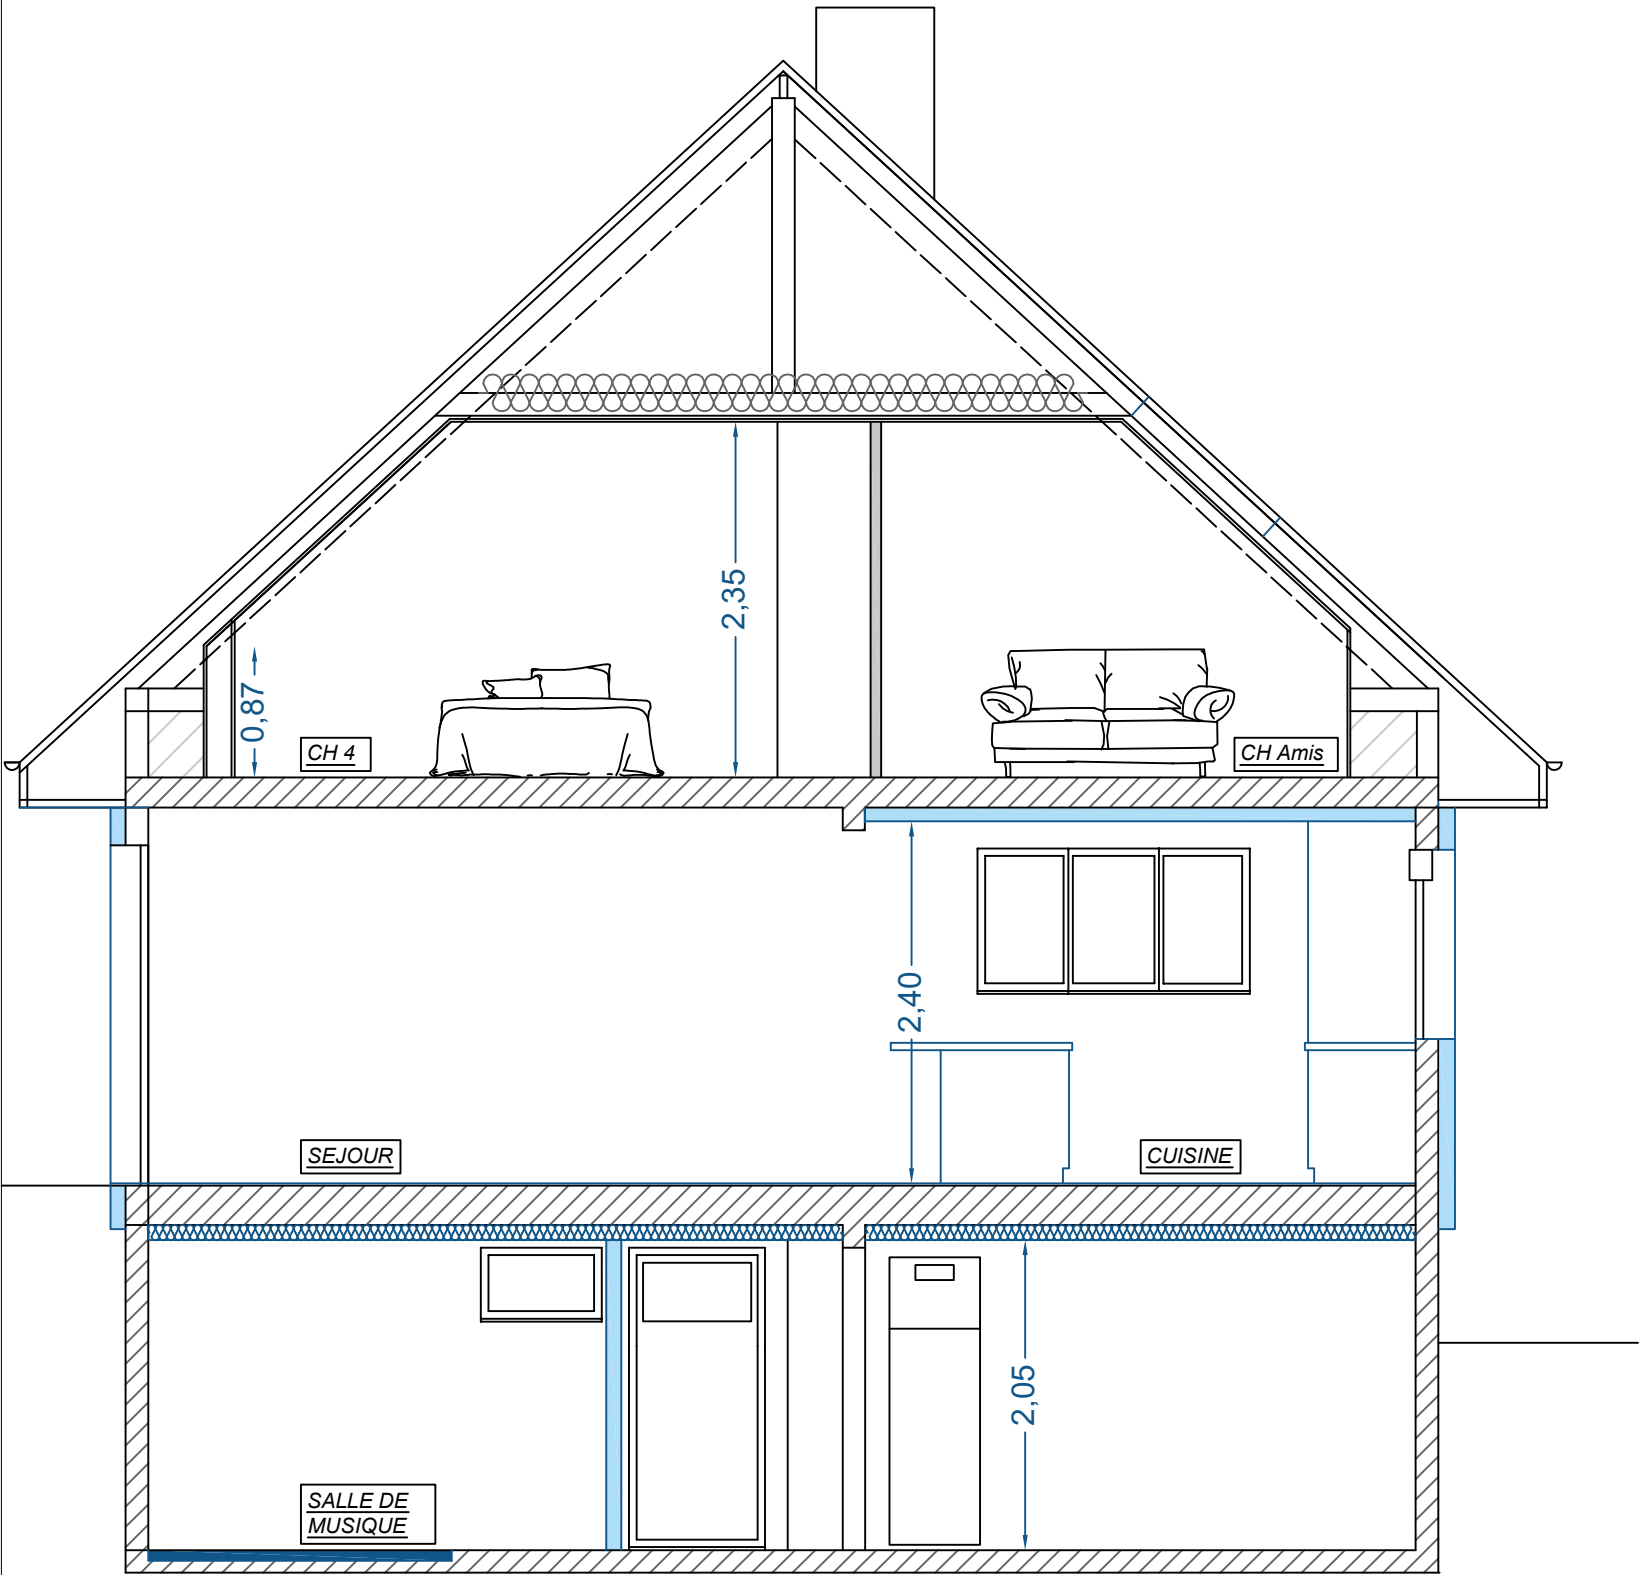

COUPE AA'

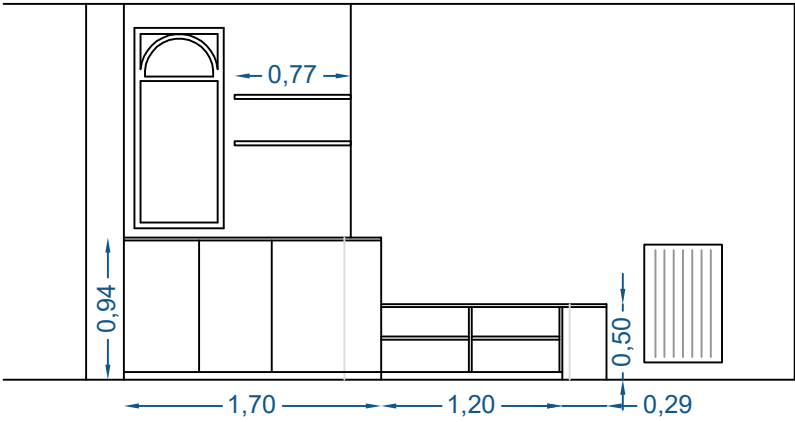

MEUBLE  
SALON



PENDERIE  
ENTRÉE

| PHASE :<br>APO                                                                                |                   |                                                                                            | N°page:<br>9                      |   |
|-----------------------------------------------------------------------------------------------|-------------------|--------------------------------------------------------------------------------------------|-----------------------------------|---|
| PROJET : Rénovation d'une habitation                                                          | Indice : 1        | Echelle : 1/50e - A3                                                                       | Charlie FRALEUX<br>06.68.07.63.68 |   |
|                                                                                               | Date : 05/05/2026 |                                                                                            |                                   |   |
|                                                                                               | COUPE AA - PROJET | MAITRE D'OEUVRE :<br>ATELIER FRALEUX<br>19 rue de la Croix Verte<br>ST JACQUES DE LA LANDE |                                   | Ces plans ne sortent pas des plans techniques de chantier et ne peuvent être utilisés en phase EXE. Les cotés doivent être repris par les lots concernés avant l'exécution de leurs ouvrages. |
| MAITRE D'OUVRAGE :<br>Céline et Amir ROCHE-SHAMAM<br>5 rue Beausoleil<br>35510 CESSON-SEVIGNÉ |                   |                                                                                            |                                   |   |

Atelier  
Fralex


- ARCHITECTURE INTÉRIEURE -  
- MAÎTRISE D'OEUVRE -

Atelier  
Fraleux


- ARCHITECTURE INTÉRIEURE -  
- MAÎTRISE D'OEUVRE -

bleu= projet


noir= existant

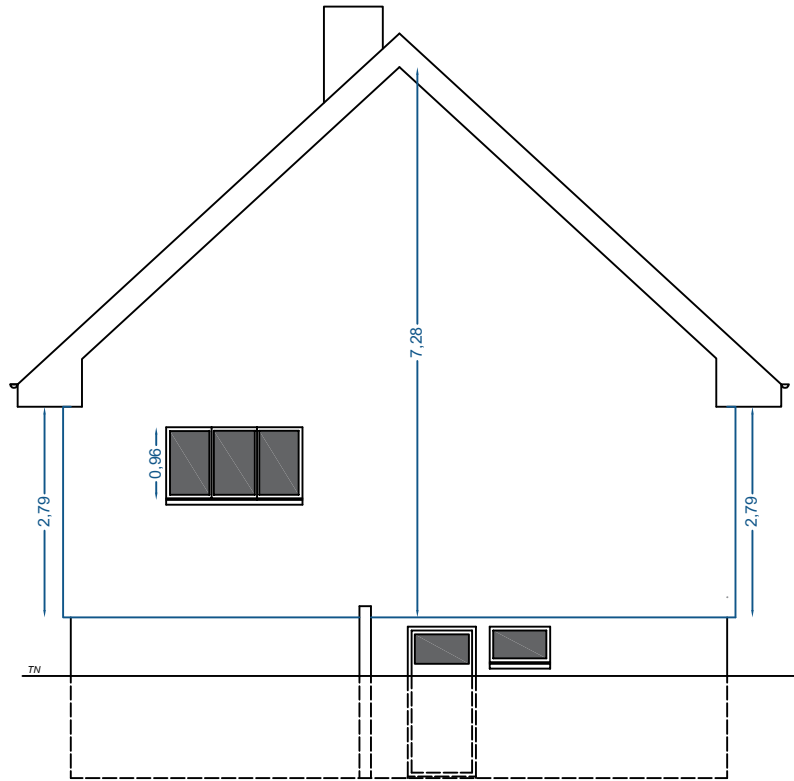

FACADE NORD

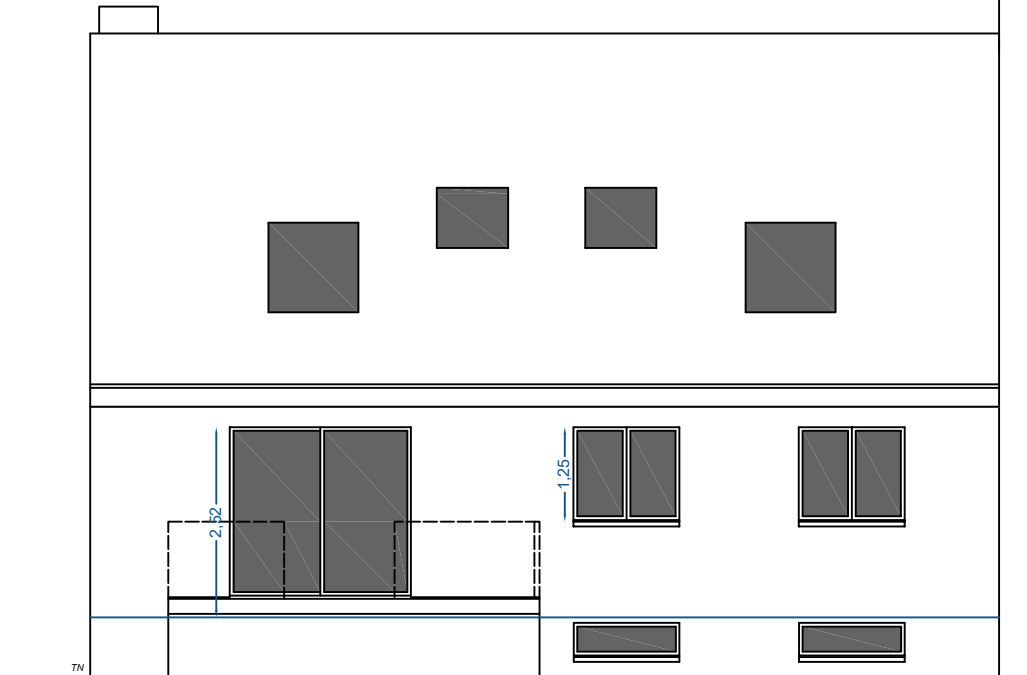

FACADE OUEST

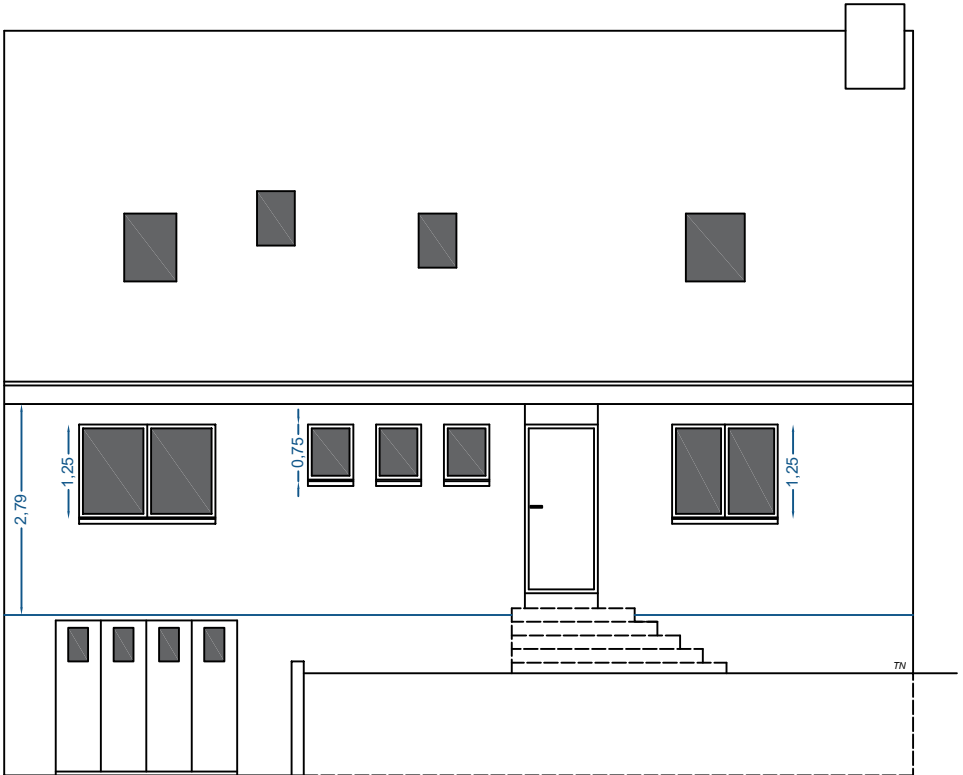

FACADE EST

|                                                                                               |  |                                                                                                   |                          |                |   |
|-----------------------------------------------------------------------------------------------|--|---------------------------------------------------------------------------------------------------|--------------------------|----------------|---|
| PROJET : Rénovation d'une habitation                                                          |  |                                                                                                   |                          | PHASE :<br>APO | N°page:<br>10   |
| FACADES- PROJET                                                                               |  | Date :<br>05/05/2026                                                                              | Echelle :<br>1/100e - A3 | Indice : 1     | Charlie FRALEUX<br>06.68.07.63.68<br><small>Ces plans ne sont pas des plans techniques de chantier et ne peuvent être utilisés en phase EXE.<br/>Les cotes doivent être reprises par les lots concernés avant l'exécution de leurs ouvrages.</small> |
| MAITRE D'OUVRAGE :<br>Céline et Amir ROCHE-SHAHAM<br>5 rue Beausoleil<br>35510 CESSON-SEVIGNÉ |  | MAITRE D'OEUVRE :<br><u>ATELIER FRALEUX</u><br>19 rue de la Croix Verte<br>ST JACQUES DE LA LANDE |                          |                |   |

Atelier  
Fralex


- ARCHITECTURE INTÉRIEURE -  
- MAÎTRISE D'OEUVRE -

Atelier  
Fraleux

- ARCHITECTURE INTÉRIEURE -  
- MAÎTRISE D'OEUVRE -

bleu= projet

noir= existant

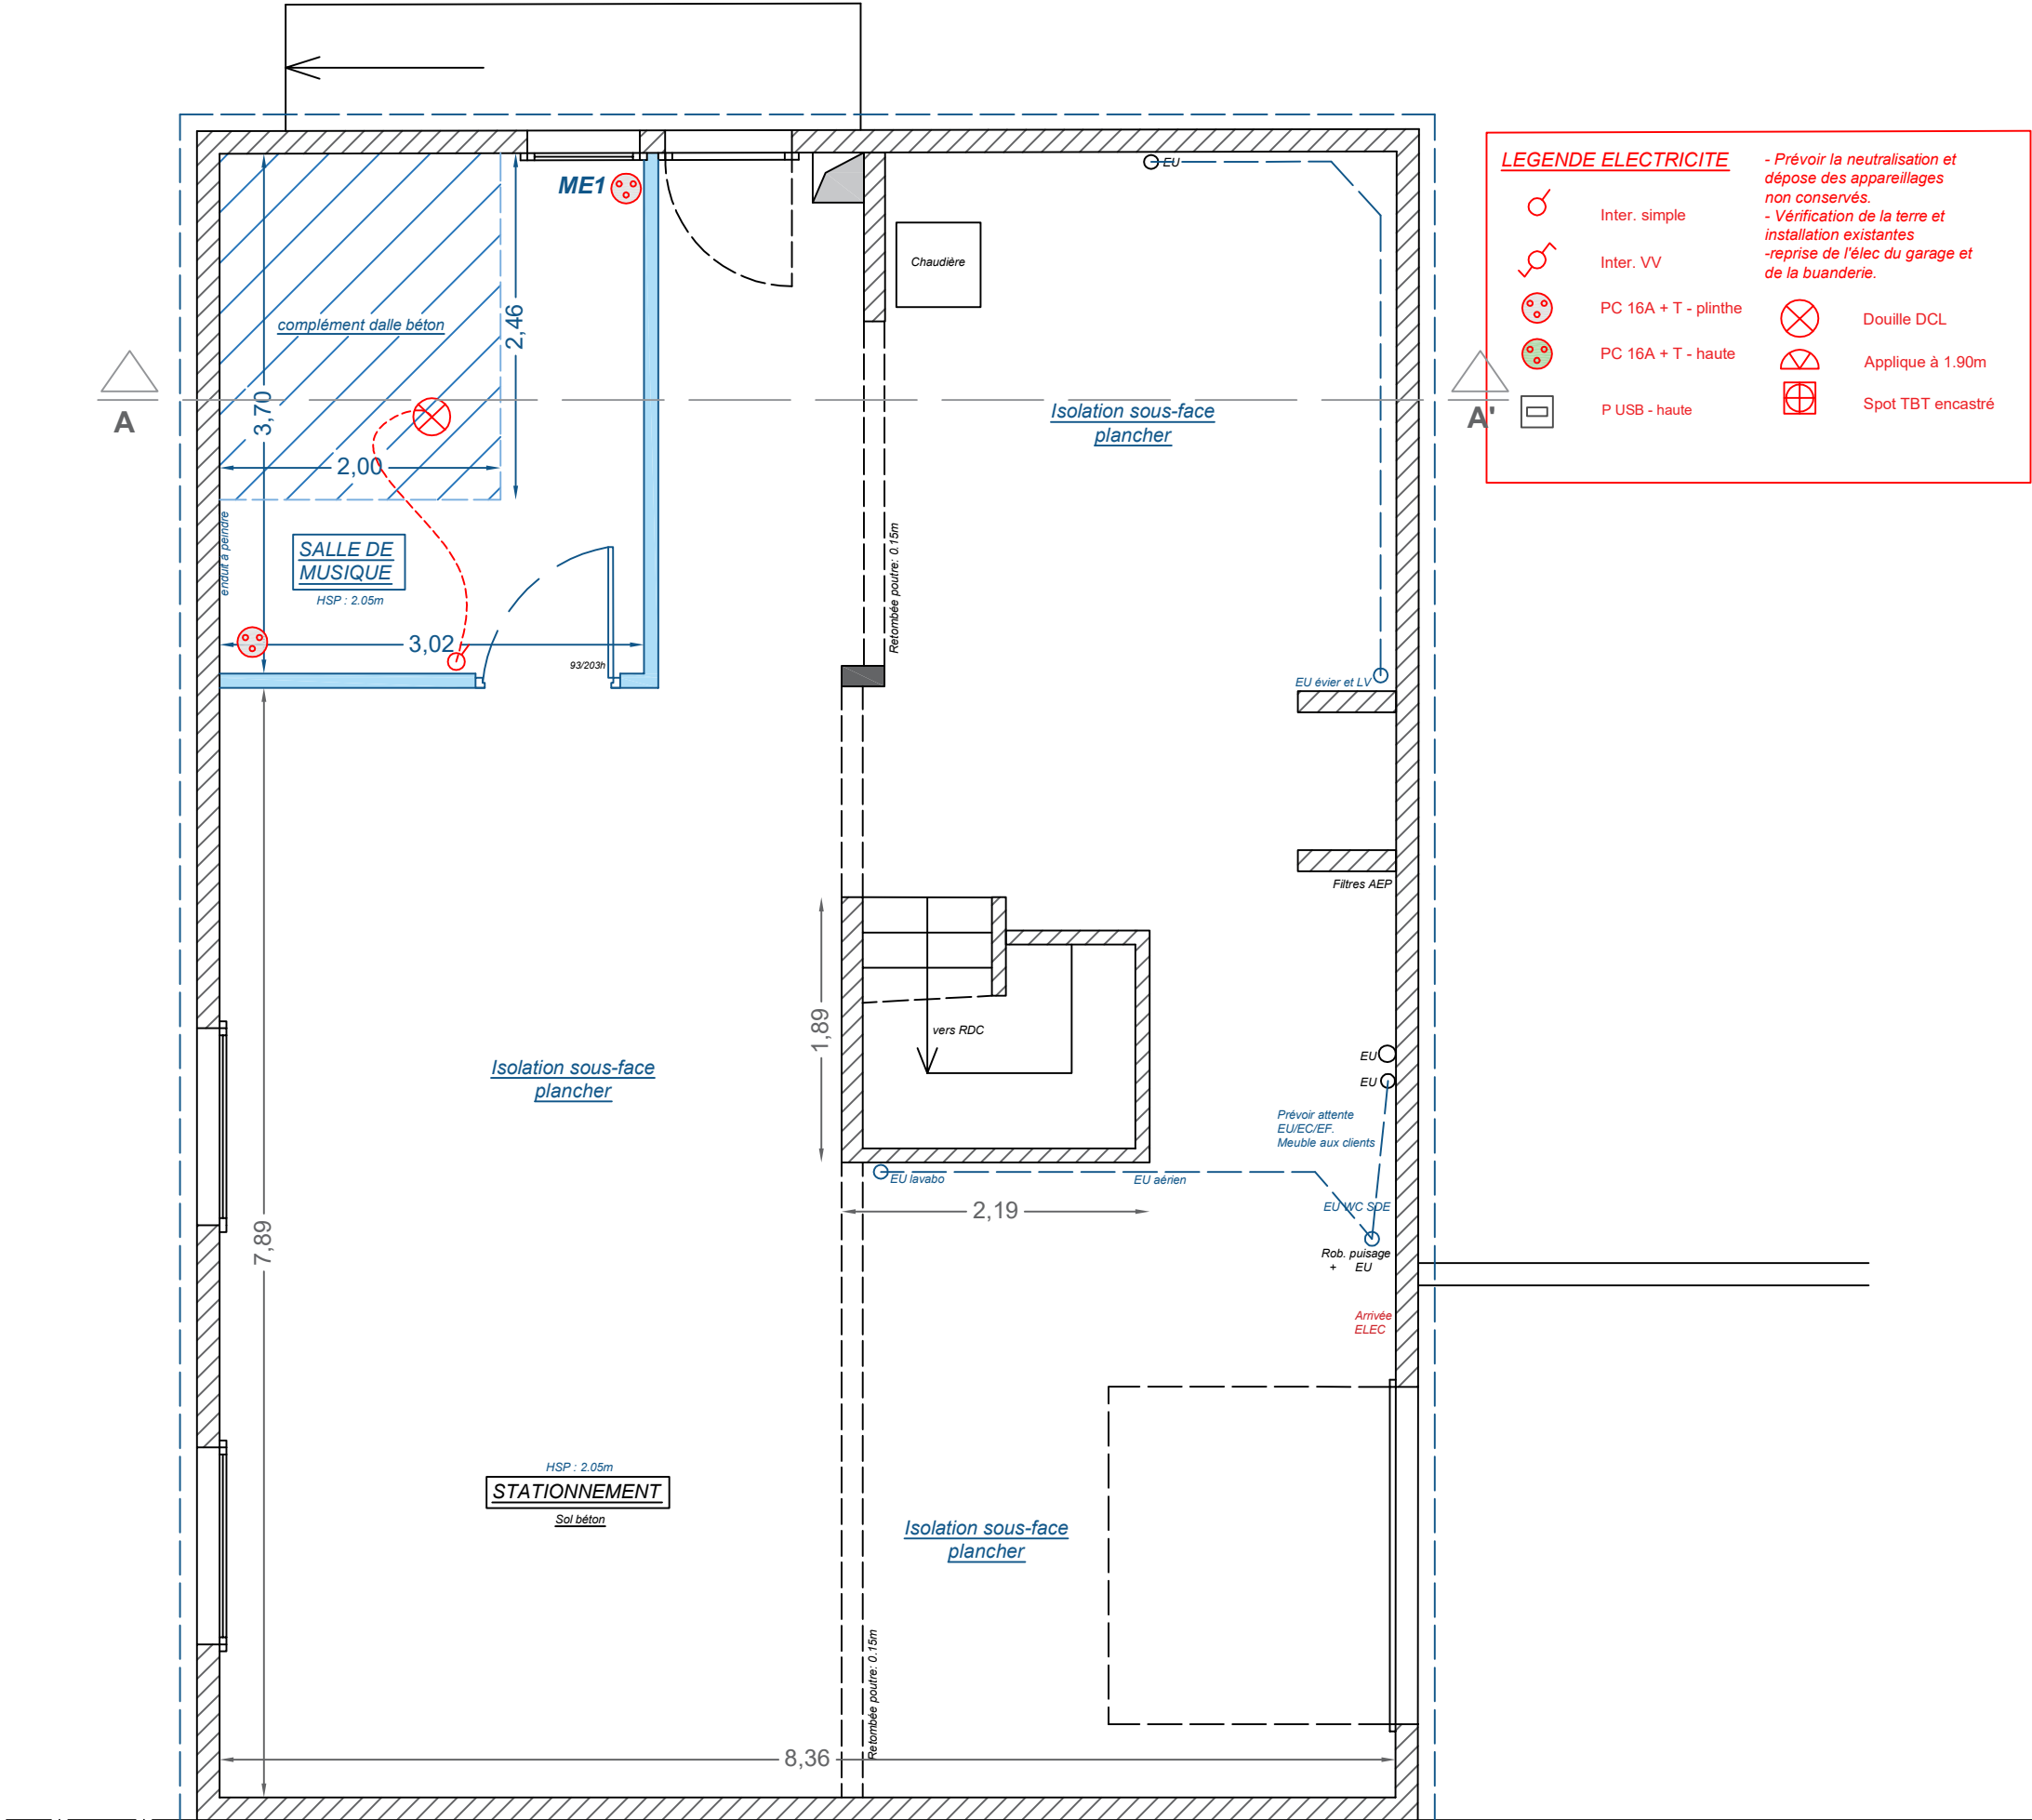

|                                                                                               |  |  |   |               |
|-----------------------------------------------------------------------------------------------|--|--|---|---------------|
| PROJET : Rénovation d'une habitation                                                          |  |  | PHASE :<br>APO   | N°page:<br>11 |
| PLAN R-1 - PROJET-ELEC                                                                        |  |  | Indice : 1   |               |
| Date : 05/05/2026                                                                             |  |  | Echelle : 1/50e - A3   |               |
| MAITRE D'OEUVRE :<br>ATELIER FRALEUX<br>19 rue de la Croix Verte<br>ST JACQUES DE LA LANDE    |  |  | Charlie FRALEUX<br>06.68.07.63.68   |               |
| MAITRE D'OUVRAGE :<br>Céline et Amir ROCHE-SHAMAM<br>5 rue Beausoleil<br>35510 CESSON-SEVIGNÉ |  |  | Ces plans ne sont pas des plans techniques de chantier et ne peuvent être utilisés en phase EXE. Les cotes doivent être reprises par les lots concernés avant l'exécution de leurs ouvrages. |               |

Atelier  
Fraleux


- ARCHITECTURE INTÉRIEURE -  
- MAÎTRISE D'OEUVRE -

bleu= projet

noir= existant

PLAN ELECTRIQUE RDC

NORD

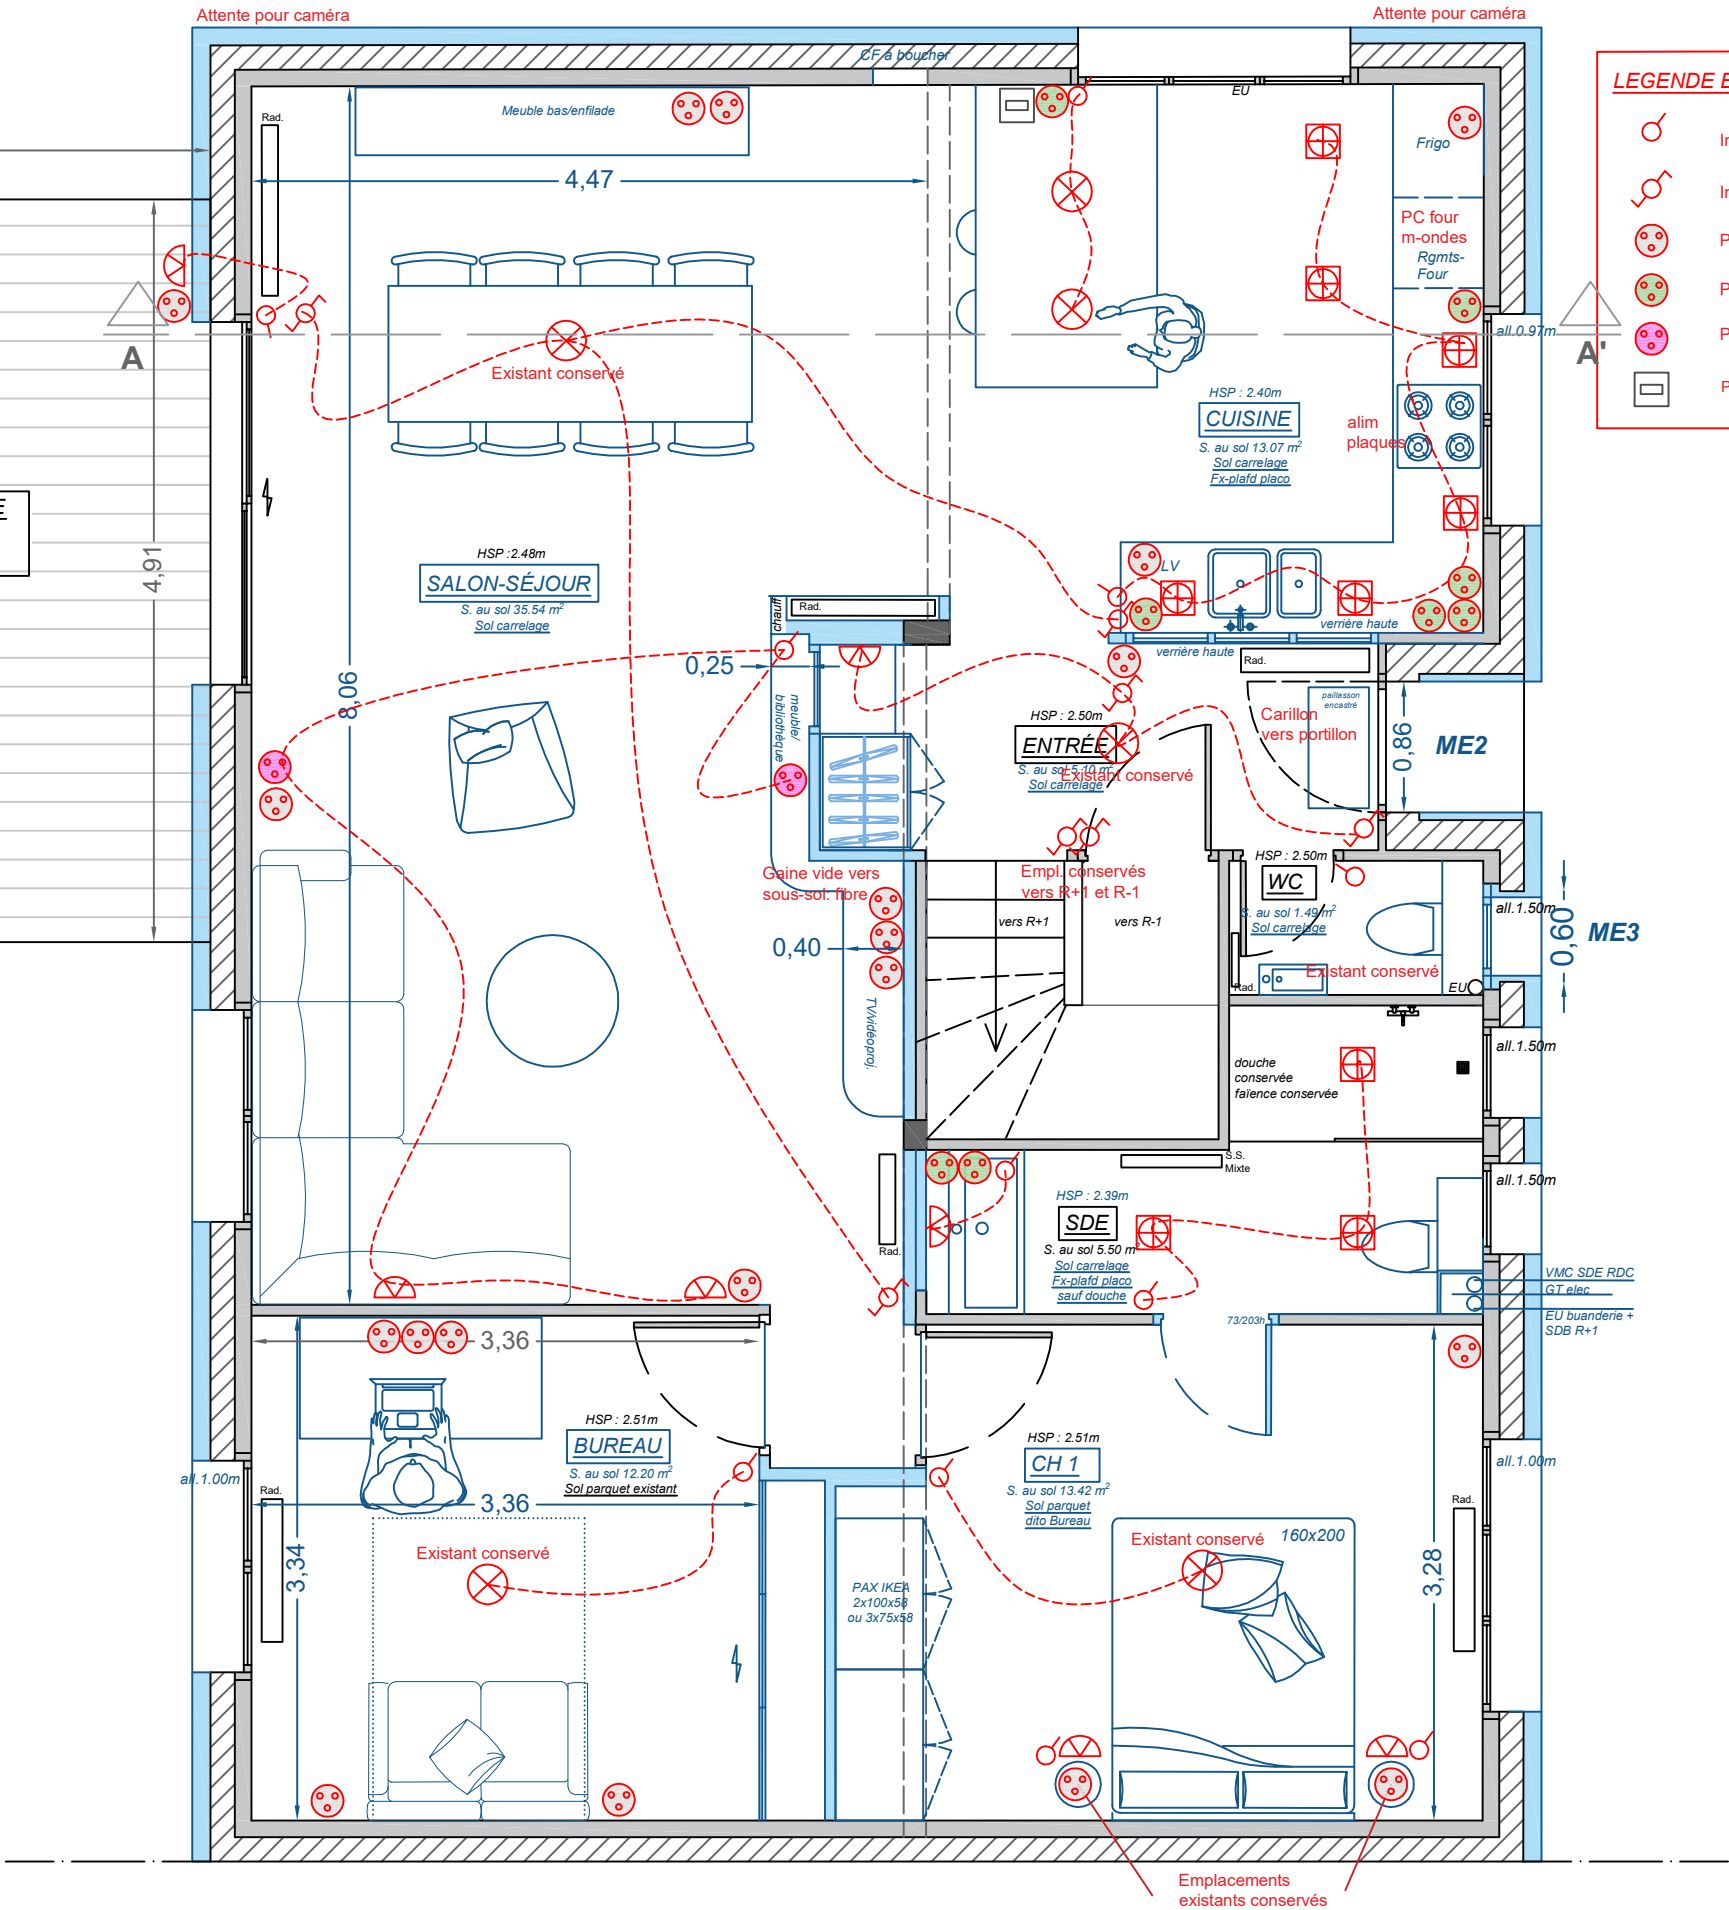

**LEGENDE ELECTRICITE**

Inter. simple

Inter. VV

PC 16A + T - plinthe

PC 16A + T - haute

PC commandée

P USB - haute

Douille DCL

Applique à 1.90m

Spot TBT encastré

- Prévoir la neutralisation et dépose des appareillages non conservés.

- Vérification de la terre et installation existantes

- reprise de l'élec du garage et de la buanderie.


|   |   |                         |                |                                                 |
|---|---|-------------------------|----------------|-------------------------------------------------|
| PROJET : Rénovation d'une habitation   |   |                         | PHASE :<br>APO | N°page:<br>12                                   |
| PLAN RDC - PROJET-ELEC   | Date :<br>05/05/2026                                                                                  | Echelle :<br>1/50e - A3 | Indice : 1     | <b>Charlie FRALEUX</b><br><b>06.68.07.63.68</b> |
|   | MAITRE D'OEUVRE :<br><br><u>ATELIER FRALEUX</u><br>19 rue de la Croix Verte<br>ST JACQUES DE LA LANDE |                         |                |                                                 |
|   | MAITRE D'OUVRAGE :<br><br>Céline et Amir ROCHE-SHAMAM<br>5 rue Beausoleil<br>35510 CESSON-SEVIGNÉ     |                         |                |                                                 |
| <div>Ces plans ne sont pas des plans techniques de chantier et ne peuvent être utilisés en phase EXE. Les cotés doivent être repris par les lots concernés avant l'exécution de leurs ouvrages.</div> |   |                         |                |                                                 |

Atelier  
Fraleux

- ARCHITECTURE INTÉRIEURE -  
- MAÎTRISE D'OEUVRE -

bleu= projet

noir= existant

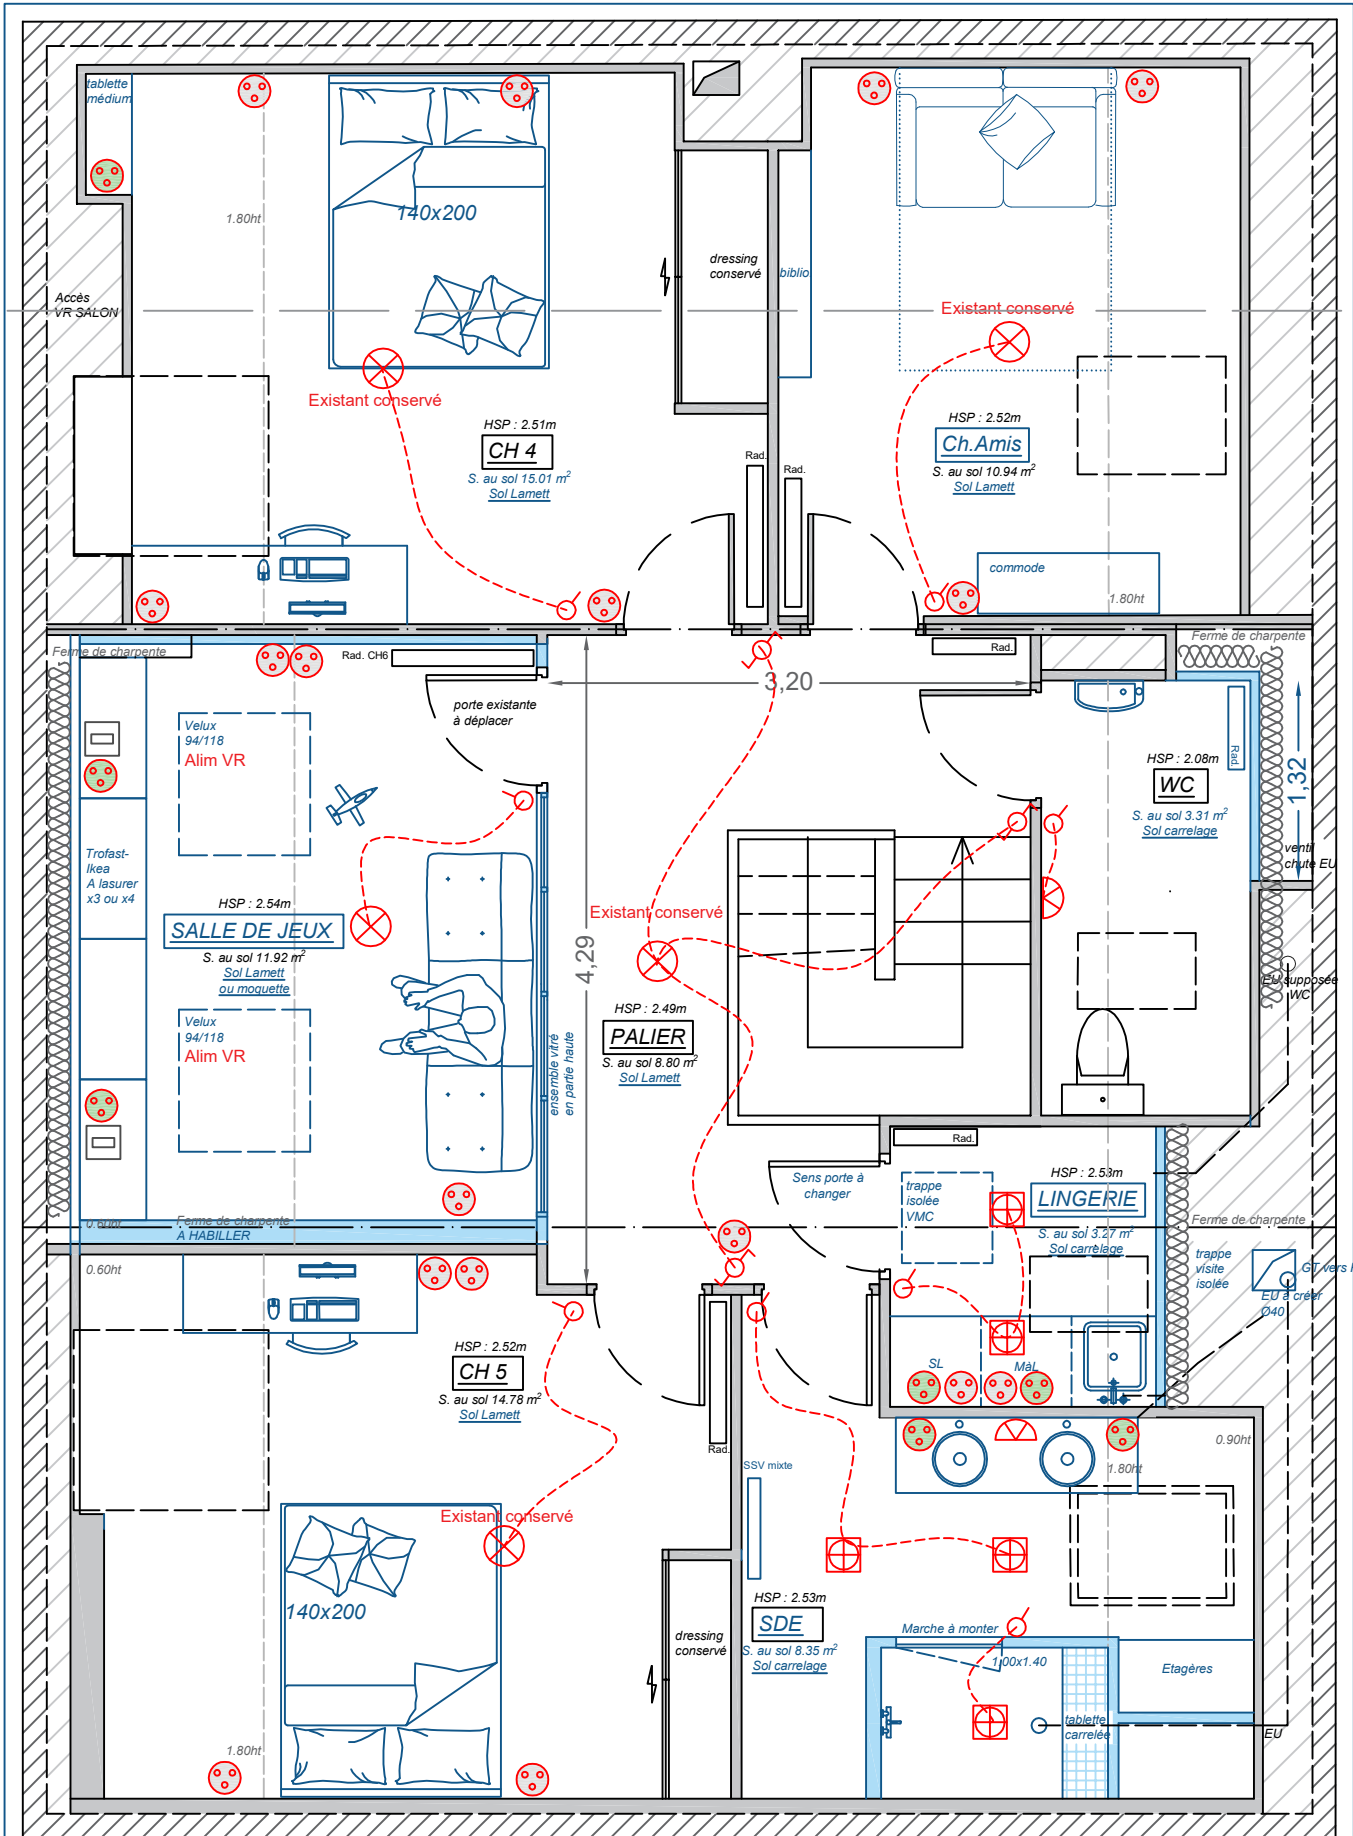

**LEGENDE ELECTRICITE**

Inter. simple

Inter. VV

PC 16A + T - plinthe

PC 16A + T - haute

P USB - haute

Douille DCL

Applique à 1.90m

Spot TBT encastré

- Prévoir la neutralisation et  
dépose des appareillages  
non conservés.  
- Vérification de la terre et  
installation existantes  
- reprise des alims des VR et VR velux

|                                                                                               |  |  |                                                                                            |                      |
|-----------------------------------------------------------------------------------------------|--|--|--------------------------------------------------------------------------------------------|----------------------|
| PROJET : Rénovation d'une habitation                                                          |  |  | PHASE :<br>APO                                                                             | N°page:<br>13        |
| PLAN R+1 - PROJET-ELEC                                                                        |  |  | Indice : 1                                                                                 | Echelle : 1/50e - A3 |
| Date : 05/05/2026                                                                             |  |  | Maitre d'oeuvre :<br>CHARLIE FRALEUX<br>06.68.07.63.68                                     |                      |
| Maitre d'ouvrage :<br>Céline et Amir ROCHE-SHAMAM<br>5 rue Beausoleil<br>35510 CESSON-SEVIGNÉ |  |  | Maitre d'oeuvre :<br>ATELIER FRALEUX<br>19 rue de la Croix Verte<br>ST JACQUES DE LA LANDE |                      |

**Atelier  
Fraleux**

- ARCHITECTURE INTÉRIEURE -  
- MAÎTRISE D'ŒUVRE -

bleu= projet

noir= existant